


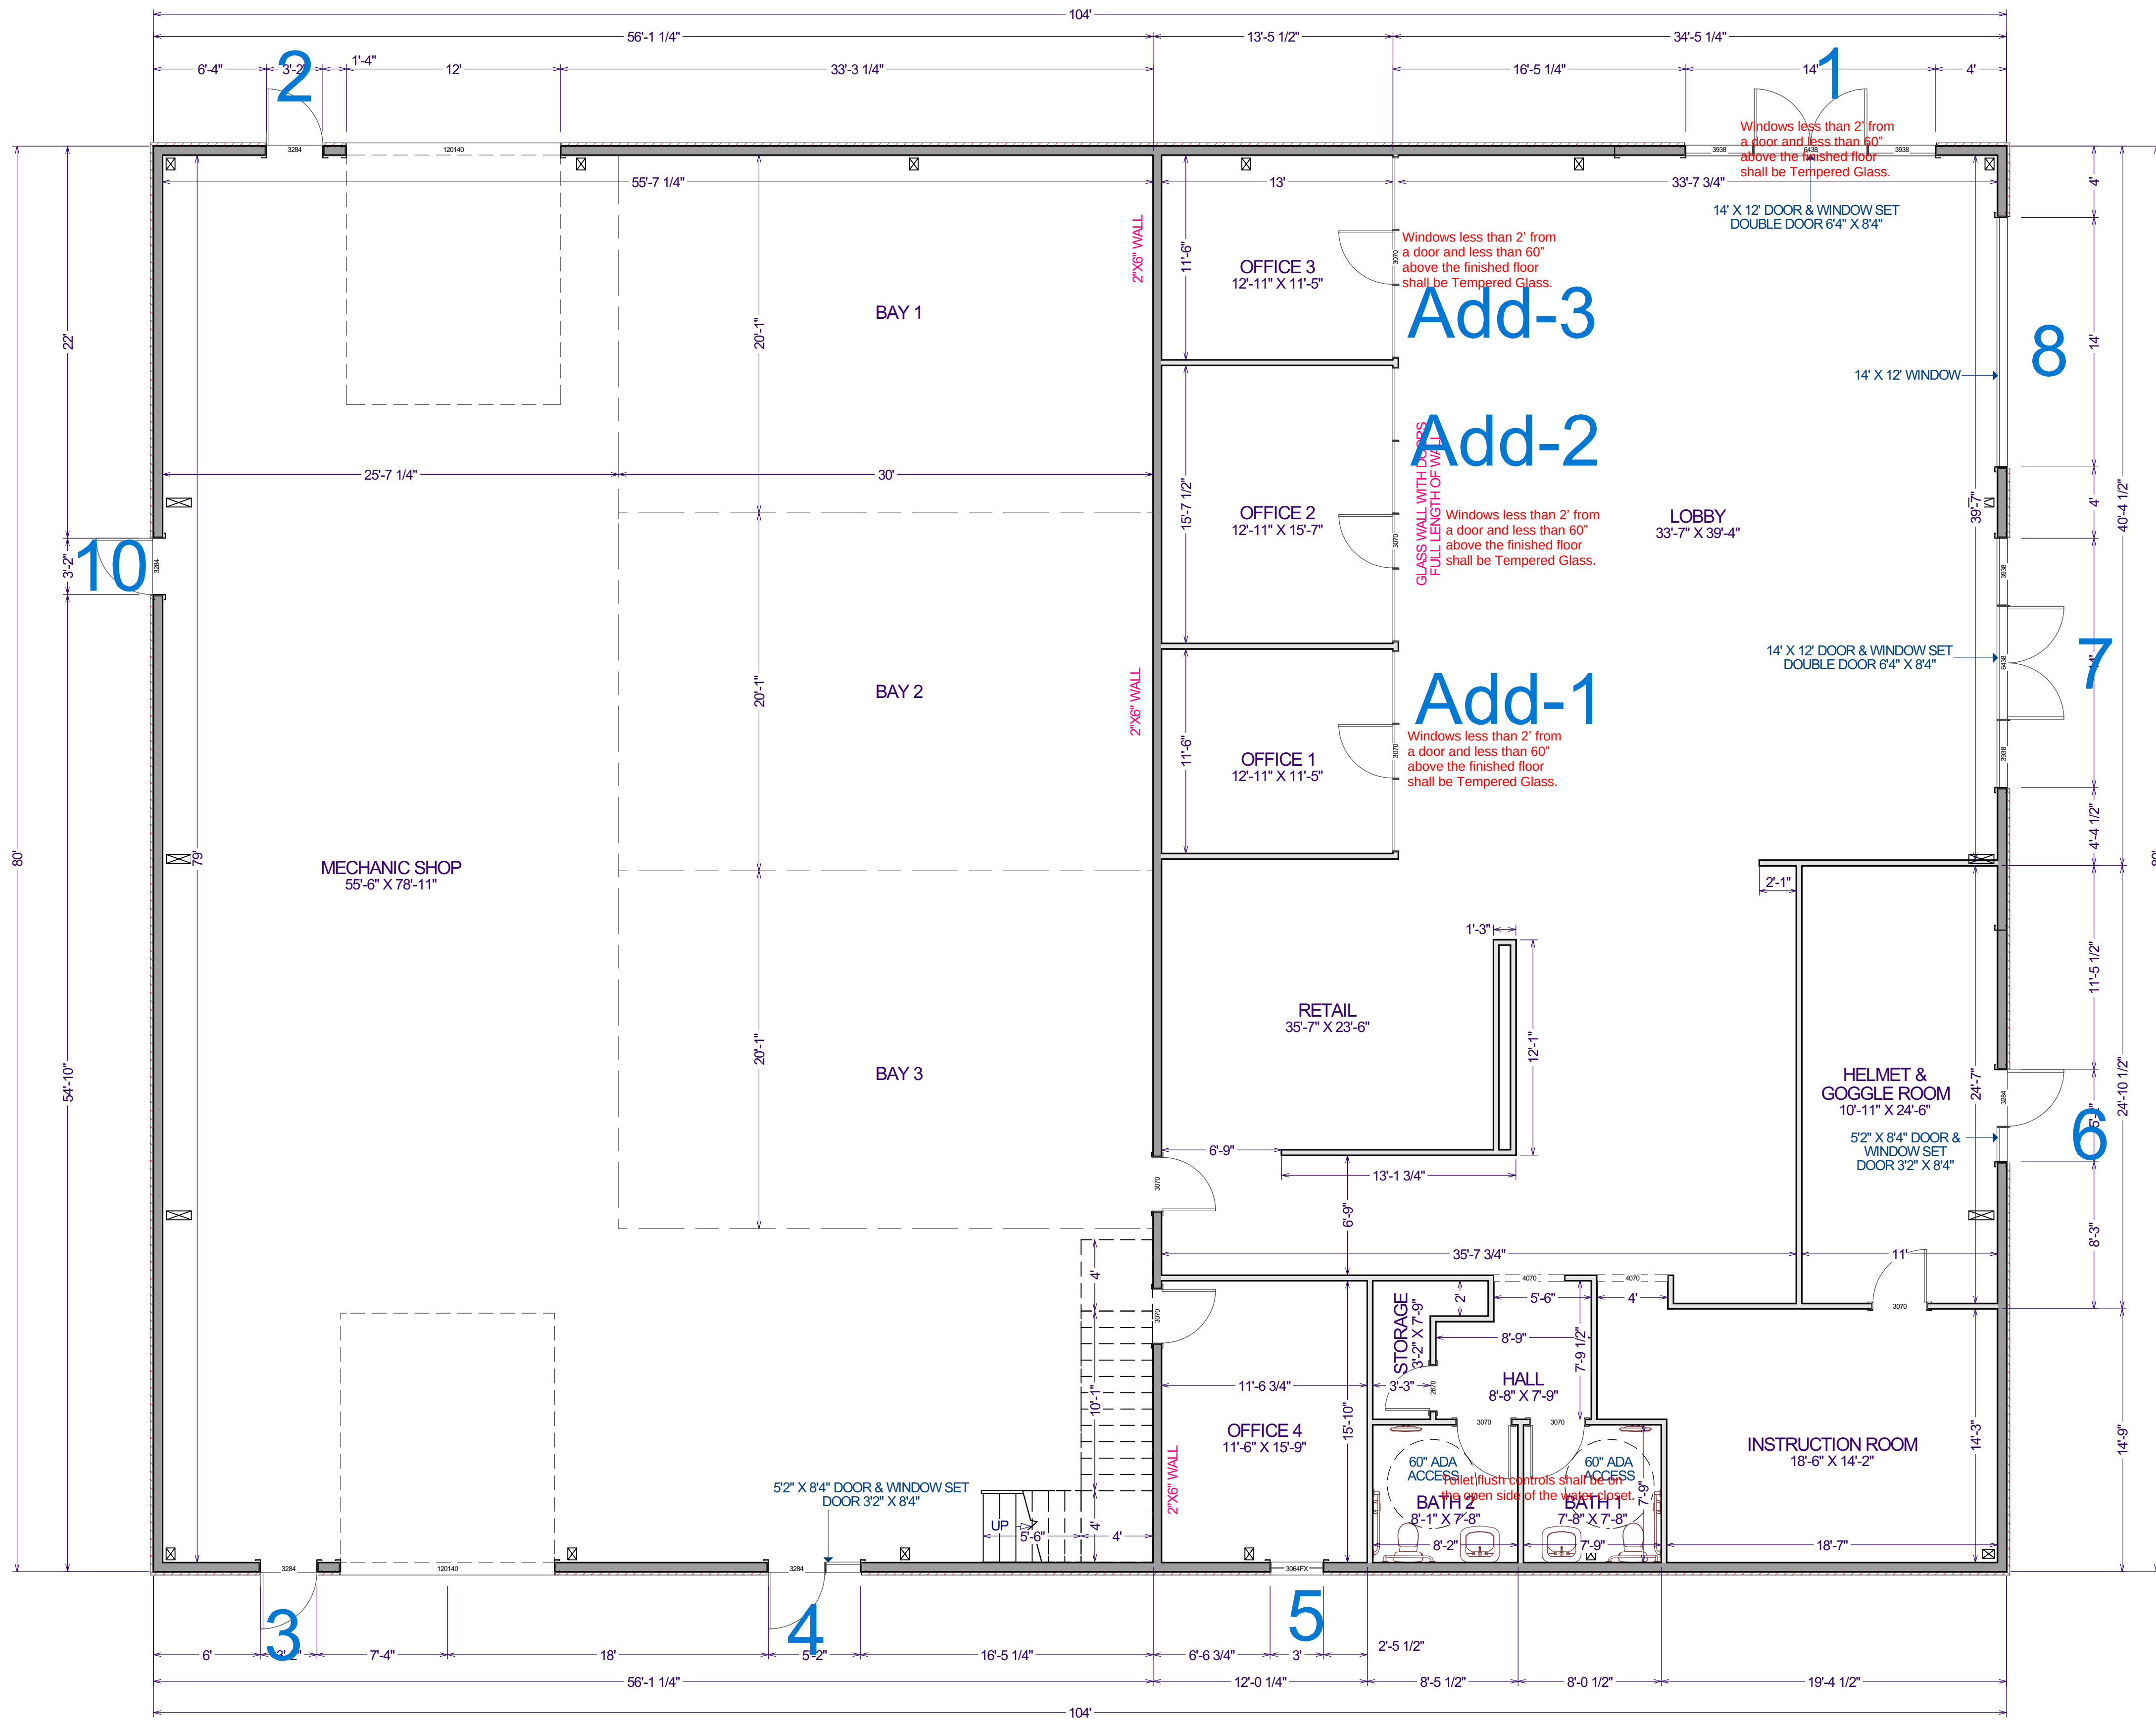

FLOOR PLAN - 1ST
3/16"= 1'

BUILDING NOTES:

- EXTERIOR WALLS: 2X6 STEEL WALL (UNLESS OTHERWISE SPECIFIED)
- INTERIOR WALLS: 2X4 WOOD WALL (UNLESS OTHERWISE SPECIFIED)
- CEILING HEIGHTS: 9' FLAT CEILING FOR MAIN FLOOR, 9' CEILING SLOPED WITH ROOF FOR SECOND FLOOR. EXCEPTION: LOBBY IS A 16' T-GRID CEILING WITH ATTIC ABOVE
- FLOOR TRUSS: 2'

STAIR DIMENSIONS:

- 1ST SECTION
- WIDTH: 4'
 - LENGTH: 5'-6"
 - TREAD DEPTH: 11"
 - TREADS: 6
 - RISER HEIGHT: 7"
- 1ST LANDING
- DIMENSION: 4'X4'
- 2ND SECTION
- WIDTH: 4'
 - LENGTH: 10'-1"
 - TREAD DEPTH: 11"
 - TREADS: 11
 - RISER HEIGHT: 7"
- 2ND LANDING
- DIMENSION: 4'X4'

HANDRAILS REQUIRED ON BOTH SIDES OF THE STAIRS.

WATCH THE OPENING REQUIREMENTS OF THE 4" AND THE 6"

ADDITIONAL DETAILS:

- WINDOW AND DOOR HEADERS ARE PROVIDED ON THE STRUCTURAL PLANS
- WINDOW AND DOOR STYLES TO BE DETERMINED BY THE OWNER
- ALL INTERIOR AND EXTERIOR MATERIALS TO BE DETERMINED BY THE OWNER

BUILDING AREA:

MAIN FLOOR: 8,320 SQ FT
SECOND FLOOR: 2,463 SQ FT

OCCUPANCY CLASSIFICATIONS:

SECTION 306 FACTORY GROUP F
306.2 MODERATE-HAZARD FACTORY INDUSTRIAL, GROUP F-1


OCCUPANCY LOAD:

- TABLE 1004.5 2021 IBC.
- SHOP, 500 SQ. FT. PER PERSON, 4,507 SQ. FT.= 9 PERSONS
 - STORAGE & MECHANICAL, 300 SQ. FT. PER PERSON, 2,128 SQ. FT.= 7.3 PERSONS
 - RETAIL, GOGGLE ROOM & LOBBY, 150 SQ. FT. PER PERSON, 2,591 SQ. FT.= 17.27 PERSONS
 - OFFICES & INSTRUCTION ROOM, 50 SQ. FT. PER PERSON, 1,048 SQ. FT.= 20.96 PERSONS
 - BREAK ROOM, 200 SQ. FT. PER PERSON, 285 SQ.FT.= 1.4 PERSONS
 - BATHROOMS, 50 SQ. FT. PER PERSONS, 224 SQ FT= 4.48 PERSONS

TOTAL 10,783 SQ. FT.= 60.41 PERSONS

CONSTRUCTION TYPE:

TYPE II-B NO FIRE SPRINKLERS

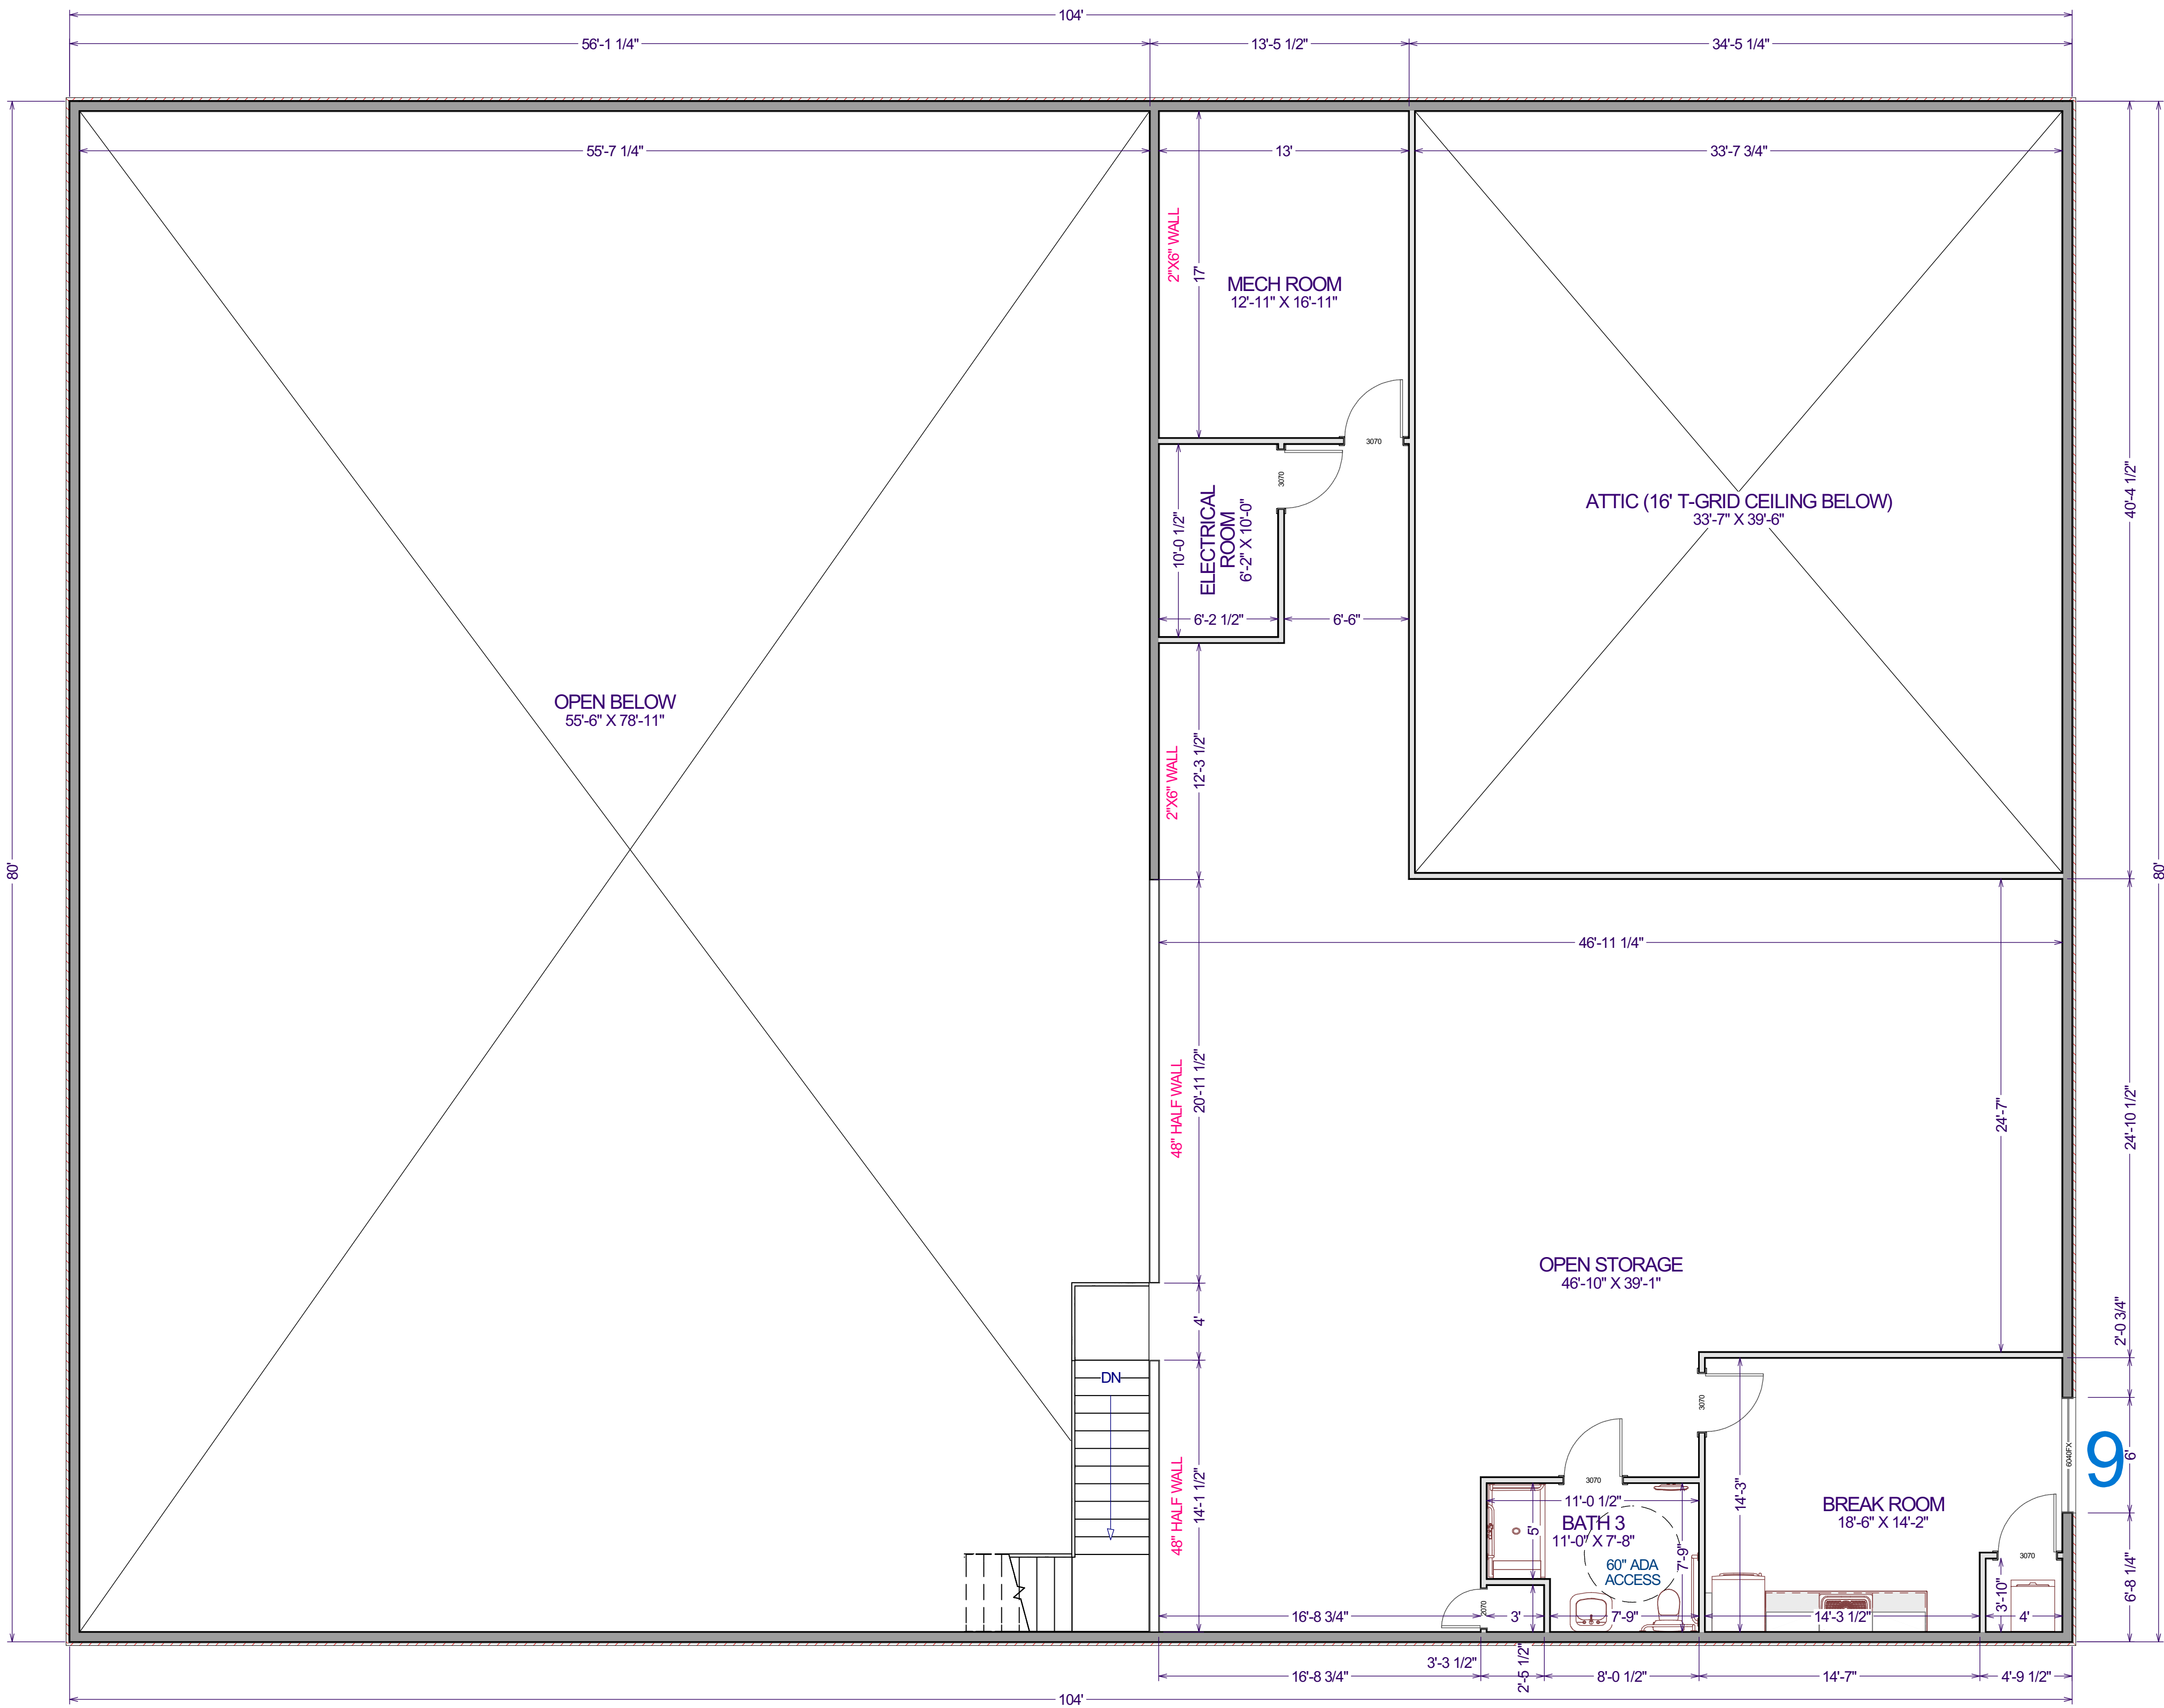

FLOOR PLAN - 2ND
3/16"= 1'

BUILDING NOTES:

- EXTERIOR WALLS: 2X6 STEEL WALL (UNLESS OTHERWISE SPECIFIED)
- INTERIOR WALLS: 2X4 WOOD WALL (UNLESS OTHERWISE SPECIFIED)
- CEILING HEIGHTS: 9' FLAT CEILING FOR MAIN FLOOR, 9' CEILING SLOPED WITH ROOF FOR SECOND FLOOR. EXCEPTION: LOBBY IS A 16' T-GRID CEILING WITH ATTIC ABOVE
- FLOOR TRUSS: 2'

ADDITIONAL DETAILS:

- WINDOW AND DOOR HEADERS ARE PROVIDED ON THE STRUCTURAL PLANS
- WINDOW AND DOOR STYLES TO BE DETERMINED BY THE OWNER
- ALL INTERIOR AND EXTERIOR MATERIALS TO BE DETERMINED BY THE OWNER



SHEET NUMBER

A5

SCALE: SEE VIEW

7/28/2025


DRAWING BY: K.R.

EXTERIOR ELEVATIONS

MAD MOOSE BUILDING
888 S SANDHOLLOW RD


PROVALUE ENGINEERING, INC.

20 South 850 West #1, Hurricane, UT 84737
435-668-8307 www.pv-eng.com

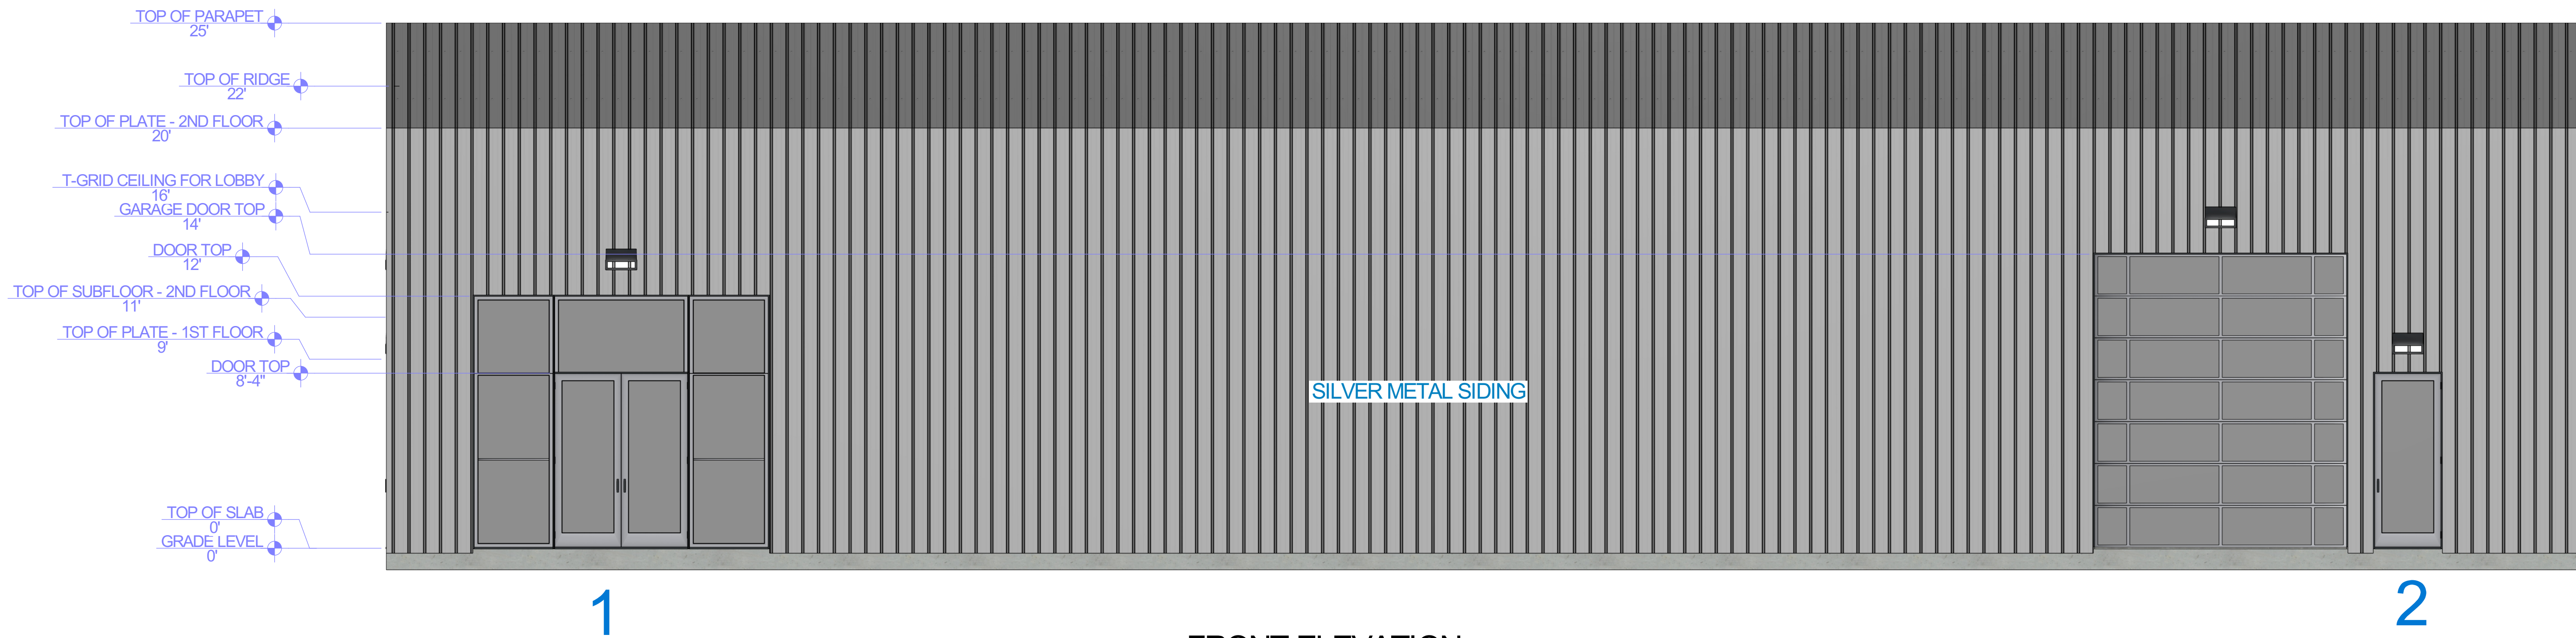

FRONT ELEVATION

1/4"= 1'

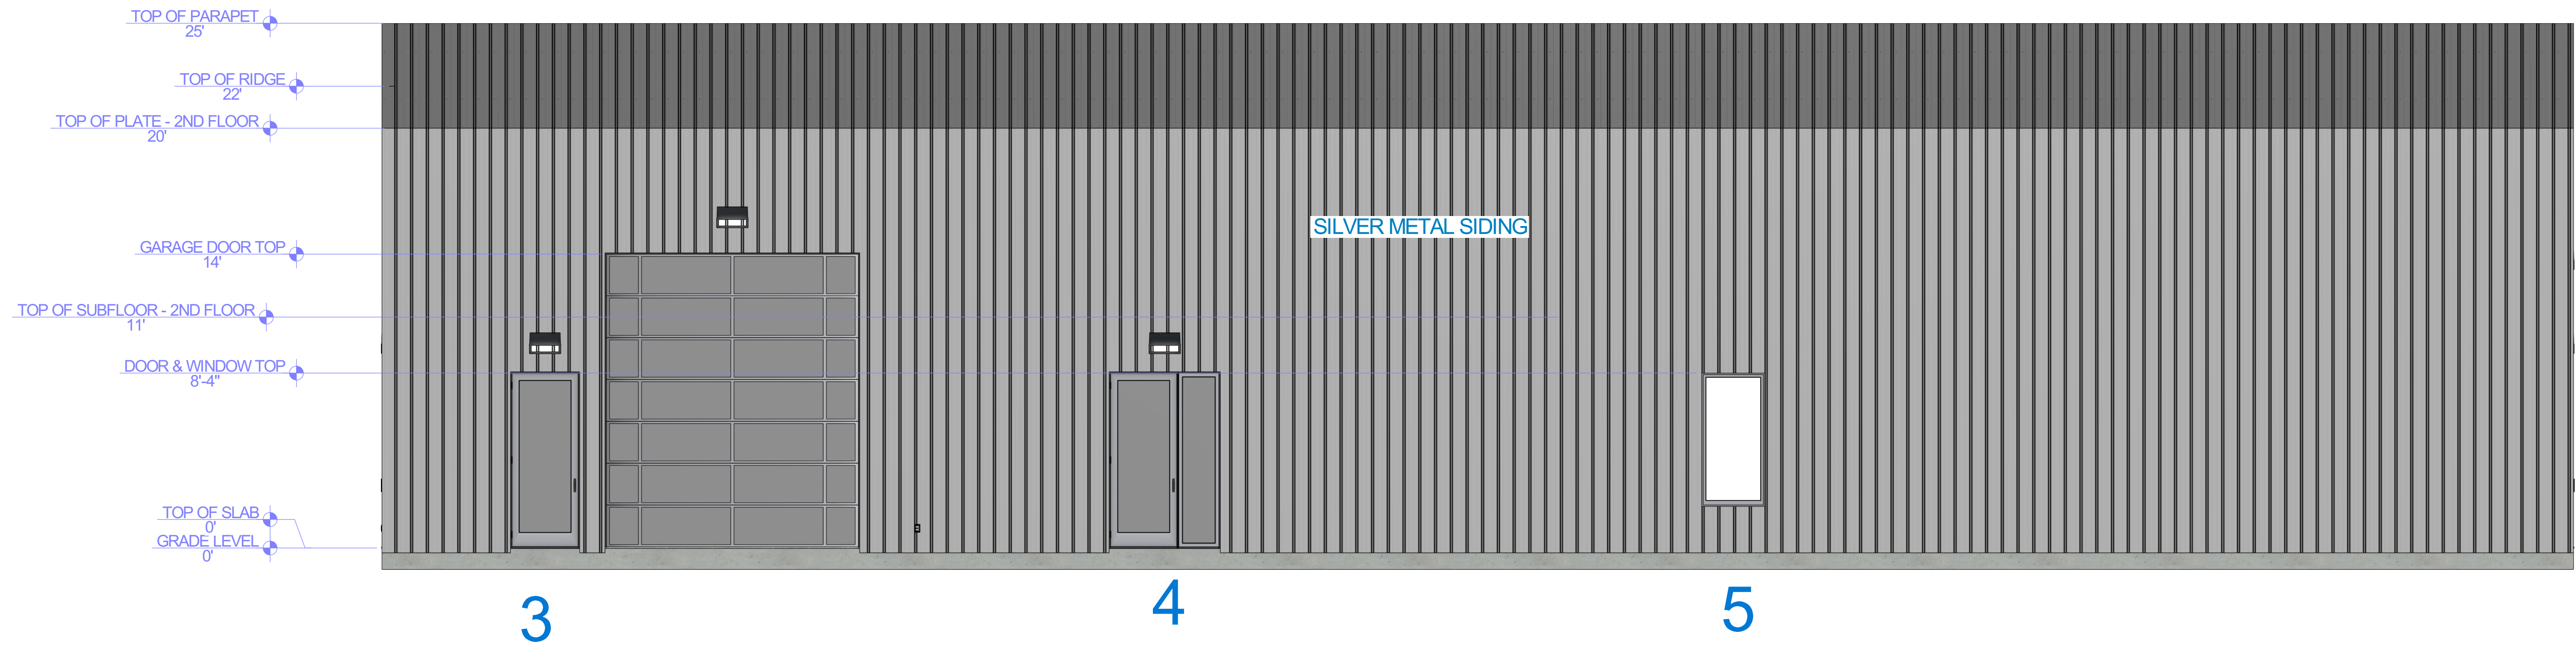

BACK ELEVATION

1/4"= 1'

SHEET NUMBER

A4

SCALE: SEE VIEW

7/28/2025

DRAWING BY: K.R.

EXTERIOR ELEVATIONS

MAD MOOSE BUILDING
888 S SANDHOLLOW RD

PROVALUE ENGINEERING, INC.

20 South 850 West #1, Hurricane, UT 84737
435-668-8307 www.pv-eng.com

