


PECAN VALLEY TOWN HOMES - BUILDING 14


LOTS 173-183, PECAN VALLEY RESORT, HURRICANE, UTAH 84737

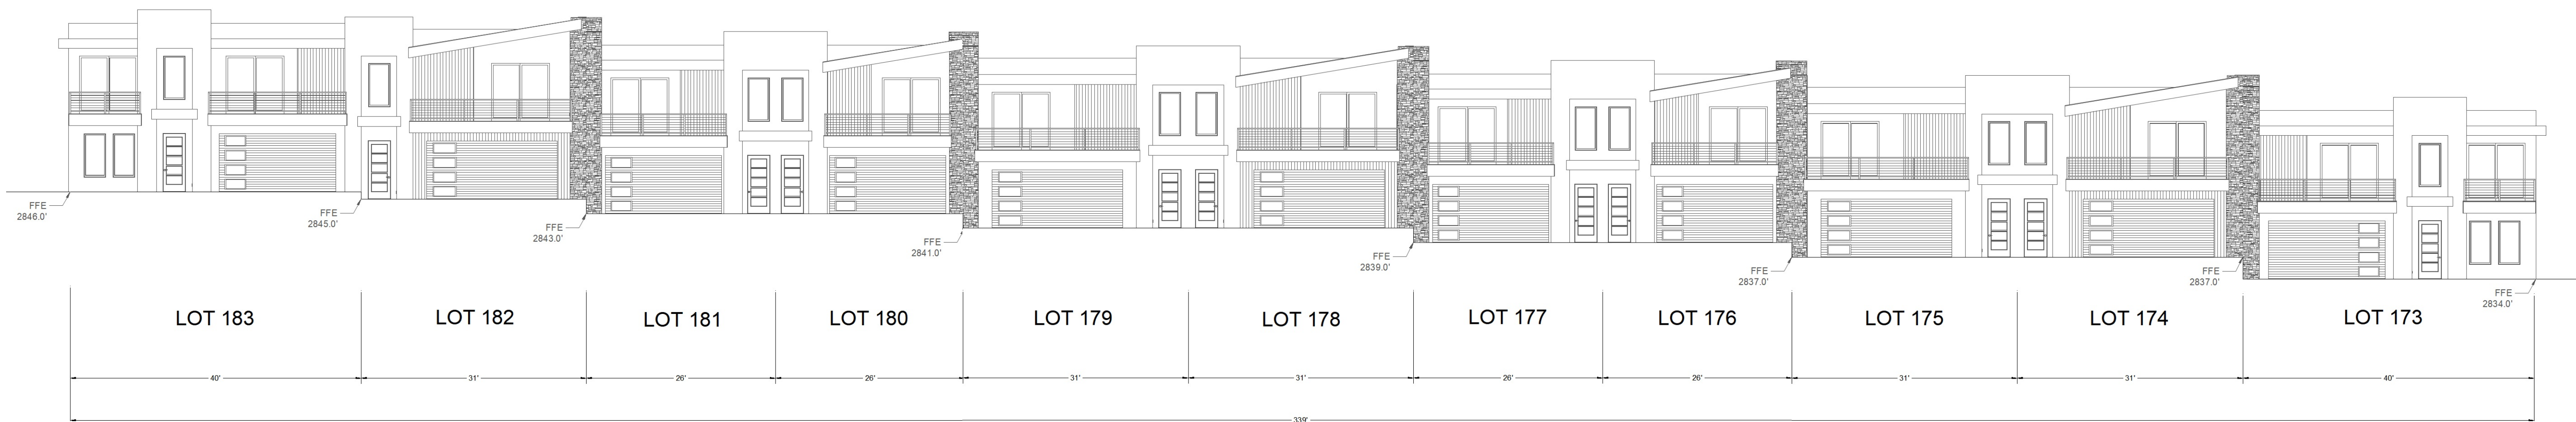

BUILDING		UNIT AREAS				PROJECT LOCATION		CONTENTS		
BUILDING WIDTH 331 FT		UNIT 173 TOTAL LIVING MAIN FLOOR UPPER FLOOR GARAGE BALCONY		5 BED / 40' 3,949 1,544 SF 1,950 SF 471 SF 348 SF		UNIT 178 TOTAL LIVING MAIN FLOOR UPPER FLOOR GARAGE BALCONY		4 BED / 31' 2,848 1,001 SF 1,483 SF 520 SF 262 SF		CS COVER SHEET
NUMBER OF UNITS 11		UNIT 174 TOTAL LIVING MAIN FLOOR UPPER FLOOR GARAGE BALCONY		4 BED / 31' 2,848 1,001 SF 1,483 SF 520 SF 262 SF		UNIT 179 TOTAL LIVING MAIN FLOOR UPPER FLOOR GARAGE BALCONY		4 BED / 31' 2,848 1,001 SF 1,483 SF 520 SF 262 SF		A1 ELEVATIONS
BUILDING AREAS:		UNIT 175 TOTAL LIVING MAIN FLOOR UPPER FLOOR GARAGE BALCONY		4 BED / 31' 2,848 1,001 SF 1,483 SF 520 SF 262 SF		UNIT 180 TOTAL LIVING MAIN FLOOR UPPER FLOOR GARAGE BALCONY		3 BED / 26' 2,123 887 SF 1,236 SF 417 212 SF		A2 FLOOR PLAN
TOTAL LIVING 27,900 SF MAIN FLOOR 11,641 SF UPPER FLOOR 16,259 SF TOTAL GARAGE 5,210 SF TOTAL BALCONY 2,926 SF		UNIT 176 TOTAL LIVING MAIN FLOOR UPPER FLOOR GARAGE BALCONY		3 BED / 26' 2,123 887 SF 1,236 SF 417 212 SF		UNIT 181 TOTAL LIVING MAIN FLOOR UPPER FLOOR GARAGE BALCONY		3 BED / 26' 2,123 887 SF 1,236 SF 417 212 SF		A3 DIMENSION PLAN
UNITS TYPES		UNIT 177 TOTAL LIVING MAIN FLOOR UPPER FLOOR GARAGE BALCONY		3 BED / 26' 2,123 887 SF 1,236 SF 417 212 SF		UNIT 182 TOTAL LIVING MAIN FLOOR UPPER FLOOR GARAGE BALCONY		4 BED / 31' 2,848 1,001 SF 1,483 SF 520 SF 262 SF		A4 ELECTRICAL PLAN
LOT 173 - 5 BED / 40' - GARAGE LEFT LOT 174 - 4 BED / 31' - GARAGE RIGHT LOT 175 - 4 BED / 31' - GARAGE LEFT LOT 176 - 3 BED / 26' - GARAGE RIGHT LOT 177 - 3 BED / 26' - GARAGE LEFT LOT 178 - 4 BED / 31' - GARAGE RIGHT LOT 179 - 4 BED / 31' - GARAGE LEFT LOT 180 - 3 BED / 26' - GARAGE RIGHT LOT 181 - 3 BED / 26' - GARAGE LEFT LOT 182 - 4 BED / 31' - GARAGE RIGHT LOT 183 - 5 BED / 40' - GARAGE RIGHT						UNIT 183 TOTAL LIVING MAIN FLOOR UPPER FLOOR GARAGE BALCONY		5 BED / 40' 3,949 1,544 SF 1,950 SF 471 SF 348 SF		A5 PLUMBING / MECHANICAL
										SP SITE PLAN
										 <u>STRUCTURAL SHEETS</u>
										S1 FOUNDATION PLAN
										S2 FRAMING PLAN
										S3 SHEAR WALL PLAN
										SD1 STRUCTURAL DETAILS




4 BEDROOM 31' WIDE UNITS

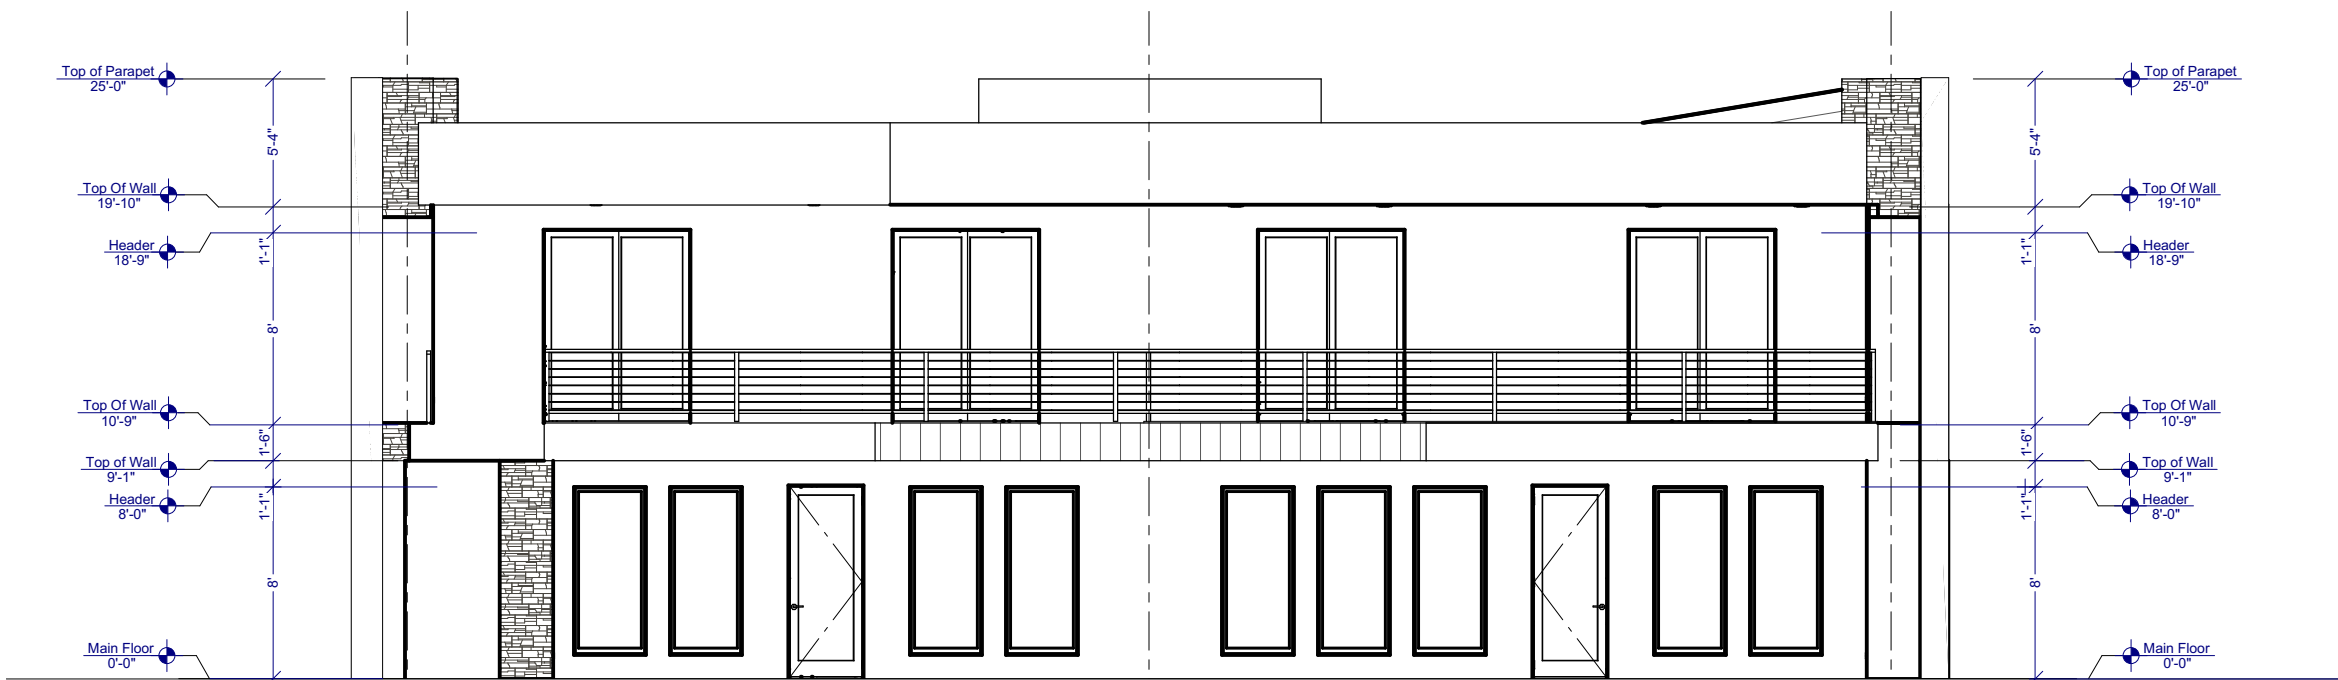


3 BEDROOM 26' WIDE UNITS



5 BEDROOM 40' WIDE UNITS

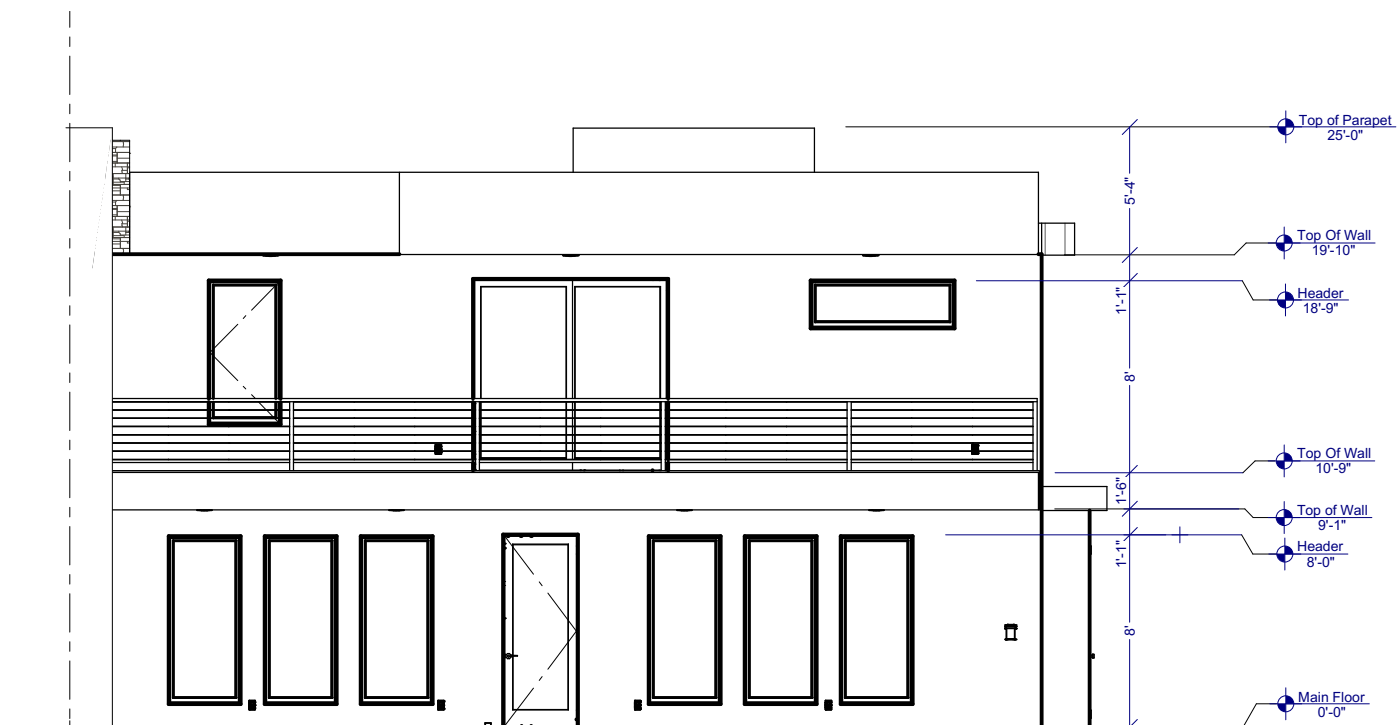


5 BEDROOM 40' WIDE UNITS

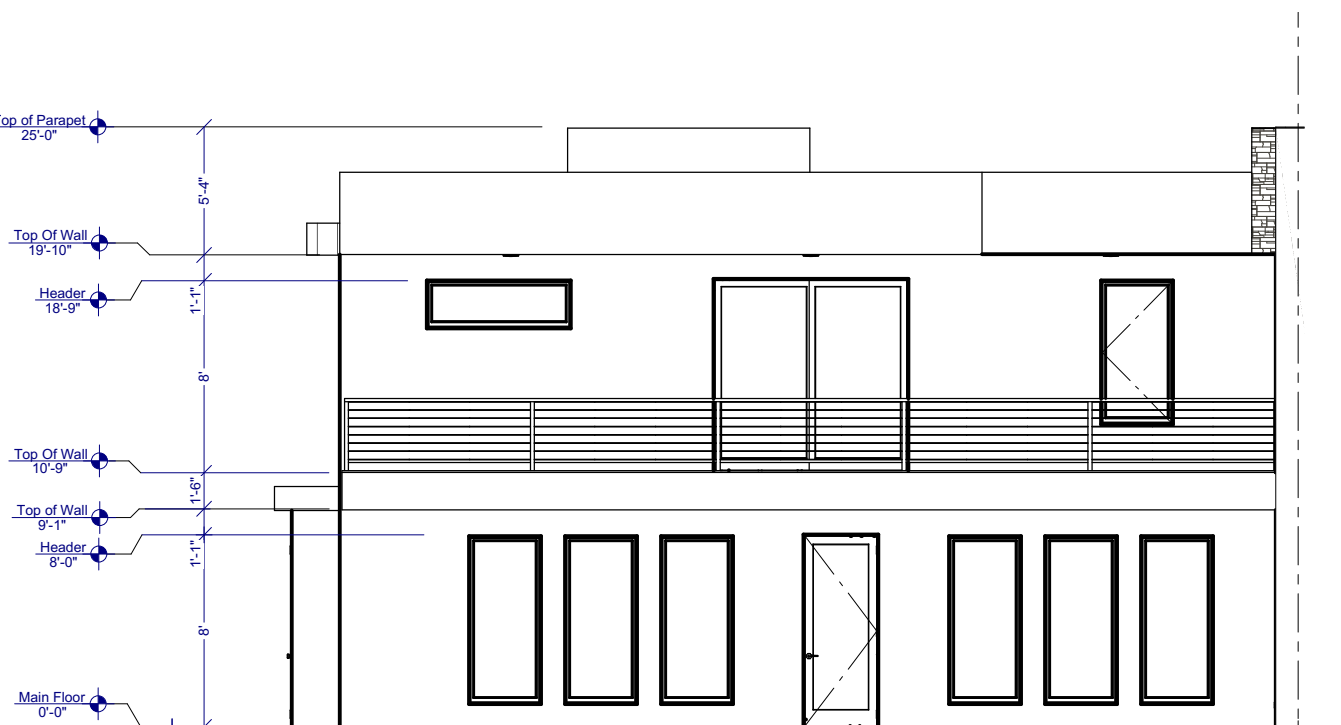

#18A 1 of 2 not used (3060 C/R)...

10

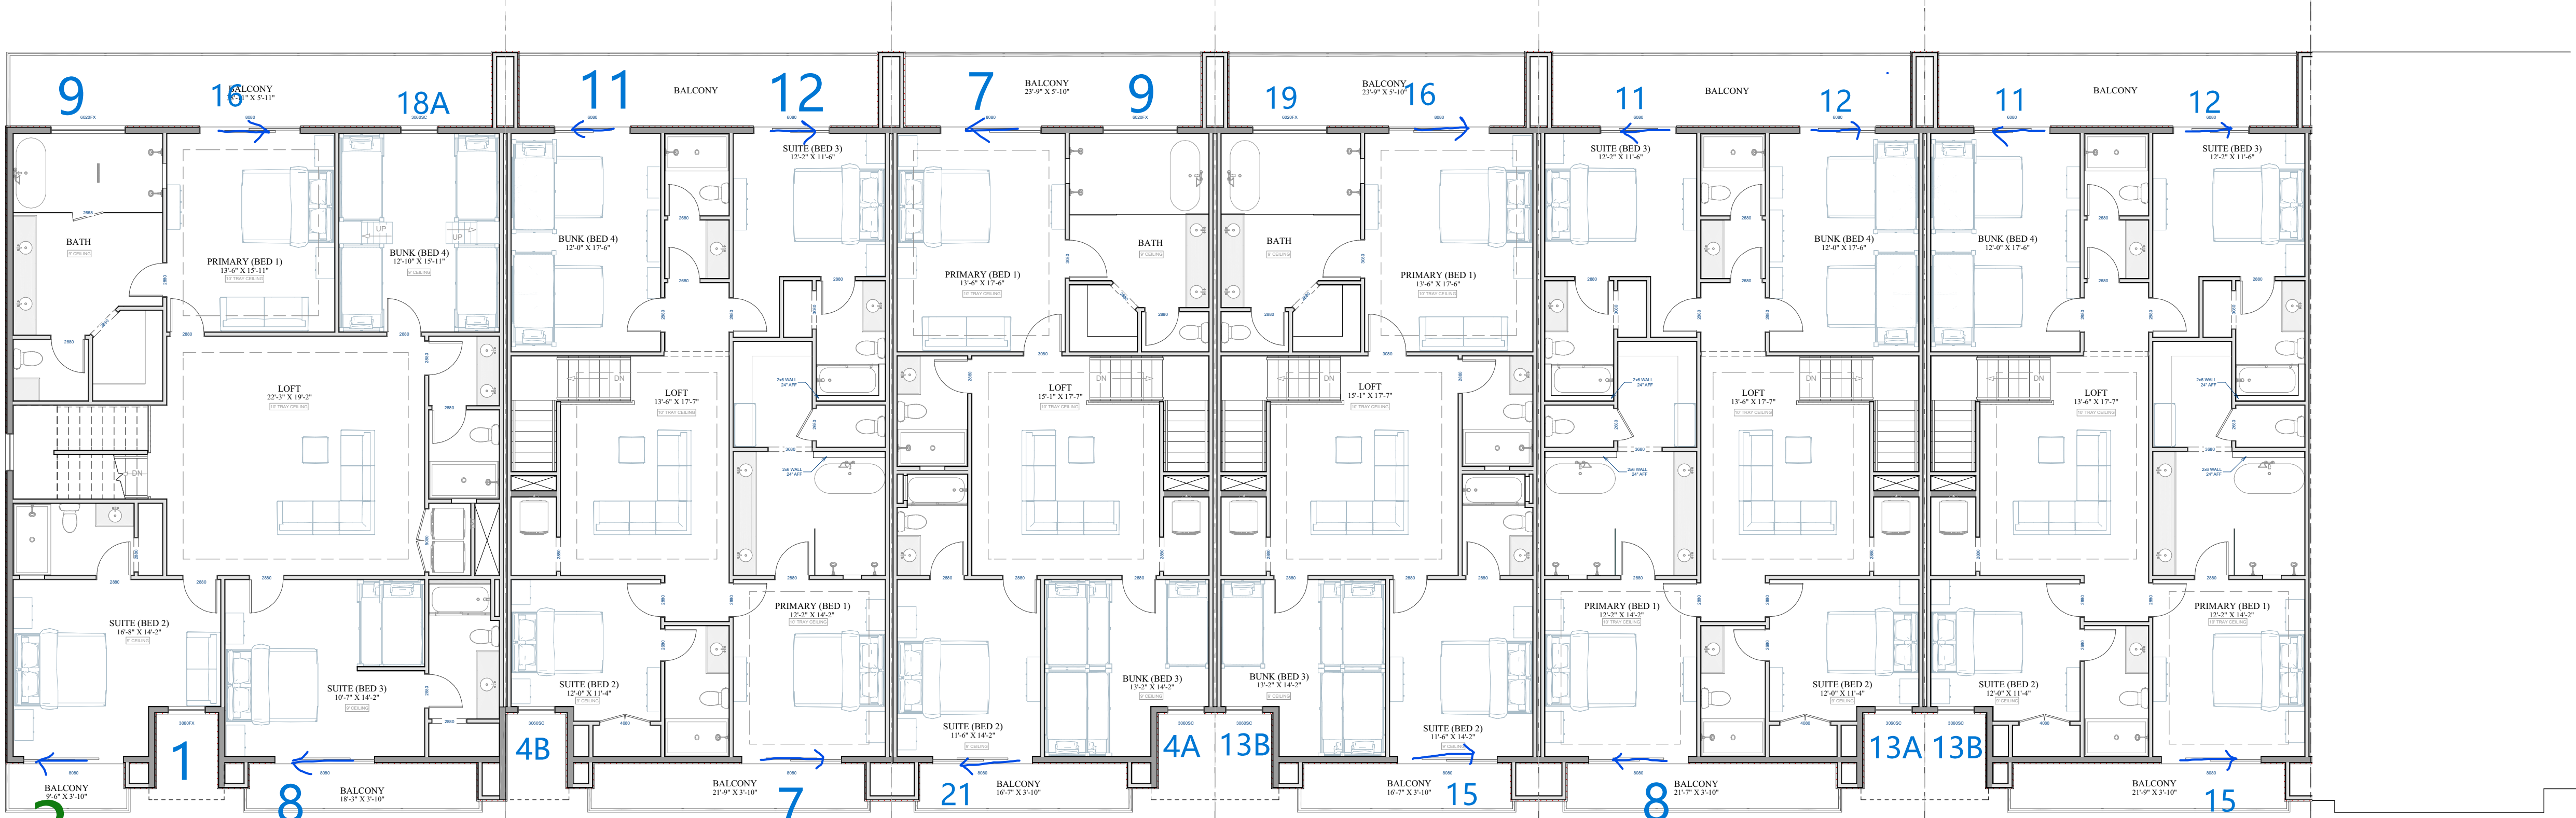

LOT 183

LOT 182

LOT 181

LOT 180

LOT 179


LOT 178

LOT 177



5

FLOOR PLAN

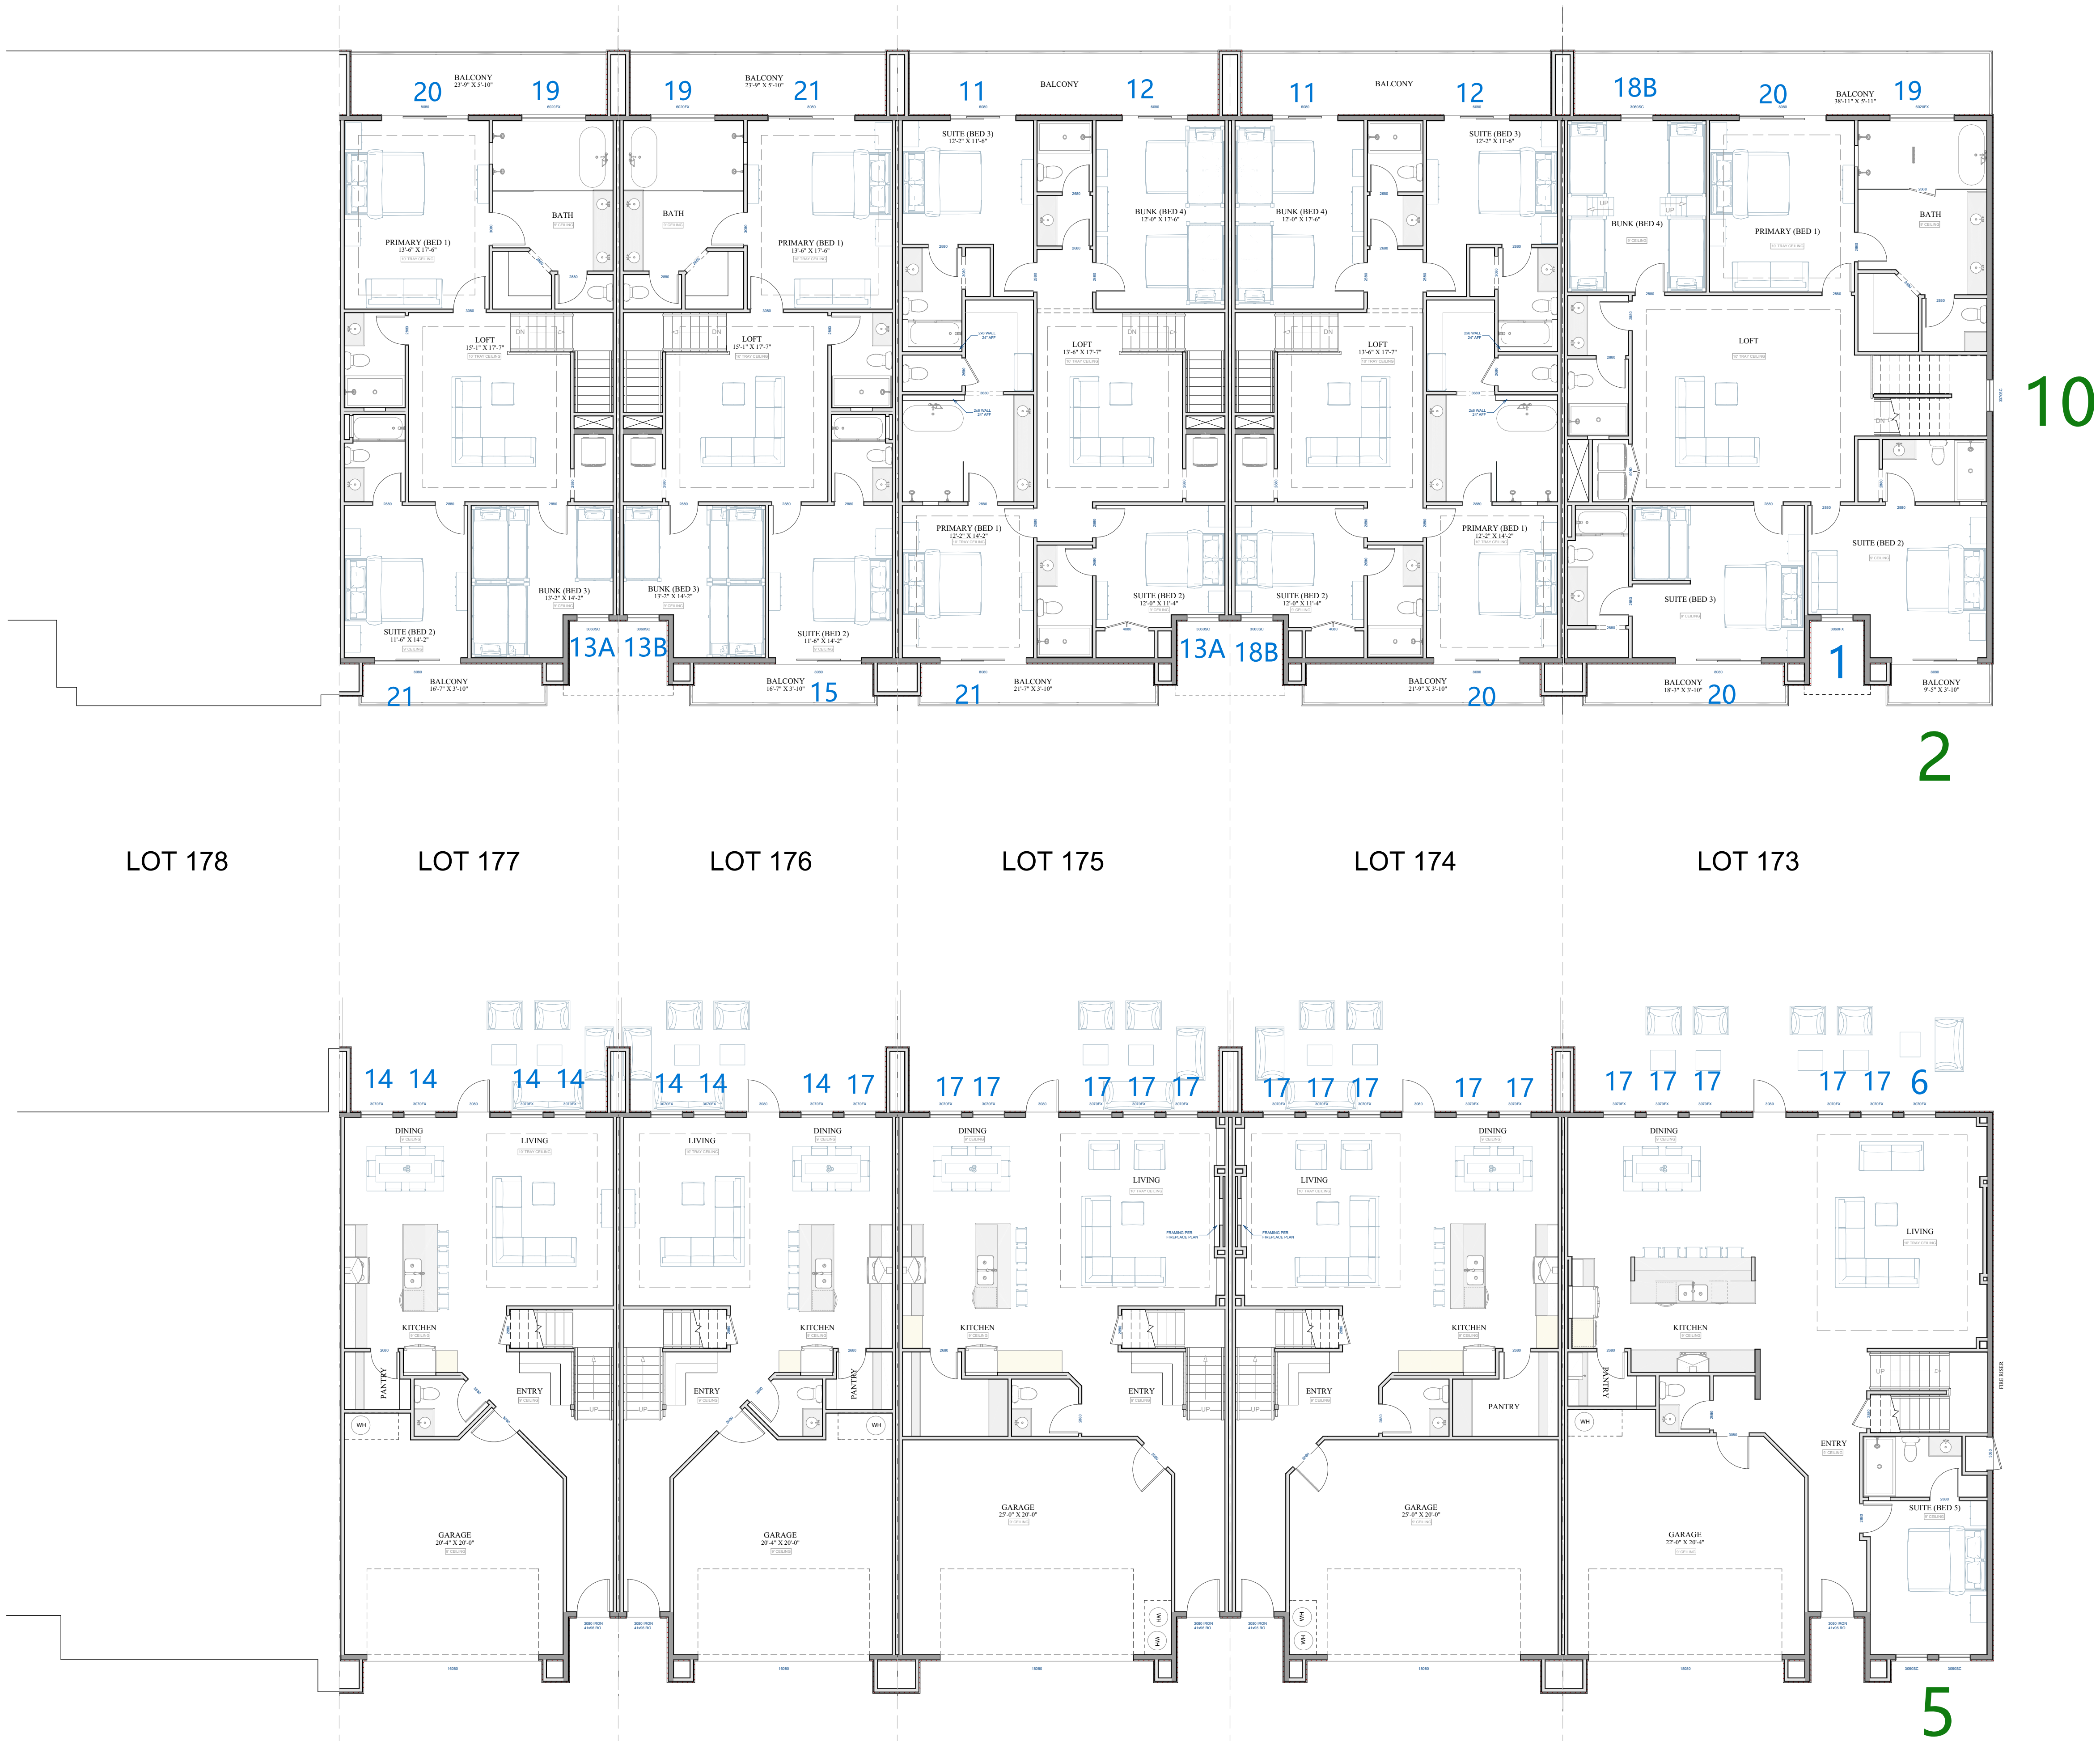

10

2

5

FLOOR PLAN