


THESE PLANS ARE THE PROPERTY OF ROUGE DESIGNS LLC. ANY REUSE OR MODIFICATION OF THESE PLANS WITHOUT THE WRITTEN PERMISSION OF ROUGE DESIGNS LLC IS STRICTLY PROHIBITED. THESE PLANS ARE THE PROPERTY OF ROUGE DESIGNS LLC. ANY REUSE OR MODIFICATION OF THESE PLANS WITHOUT THE WRITTEN PERMISSION OF ROUGE DESIGNS LLC IS STRICTLY PROHIBITED.

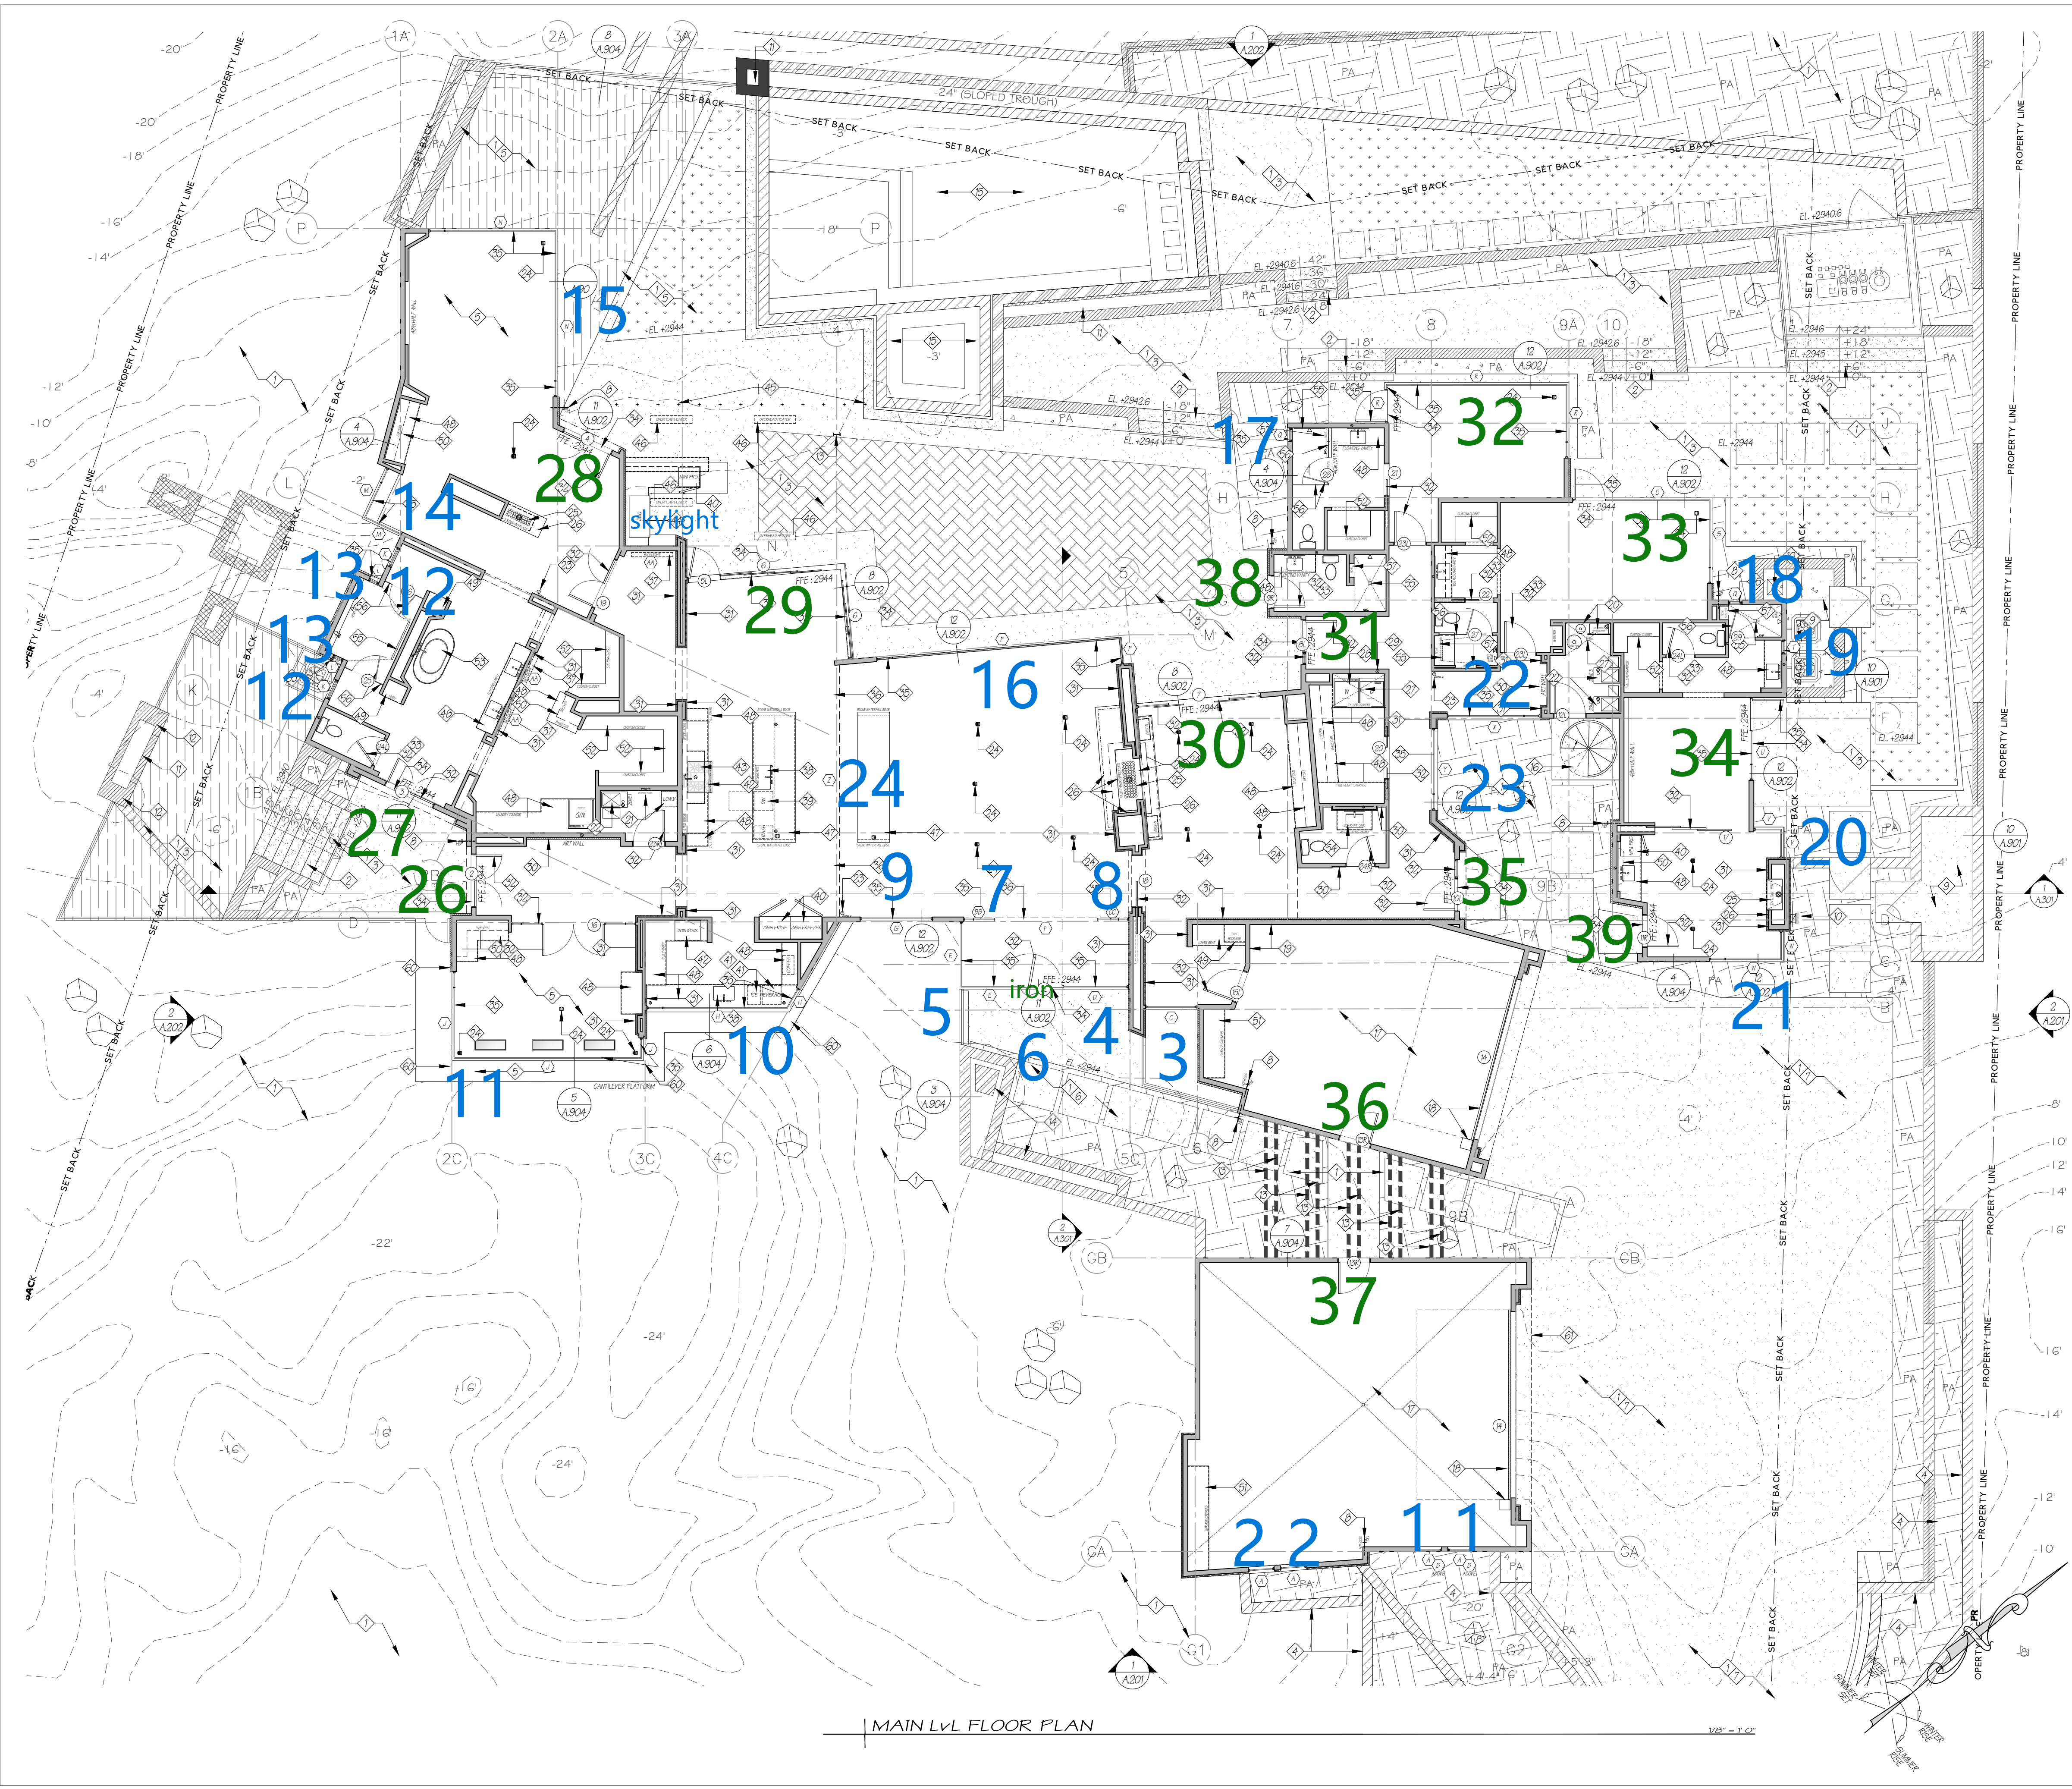

FLOOR PLAN KEYED NOTES:

- COORDINATE W/ CIVIL DRAWINGS & LANDSCAPE DRAWINGS FOR CONTINUATION OF SIDEWALKS, DRIVEWAYS, SITE WORK, PLANTER BEDS / BOXES, FLAT WORK, RETAINING WALLS, AND OTHER SITE REQUIREMENTS.
- EXTERIOR OUTDOOR STEPS & LANDING FIELD VERIFY FOR AMOUNT OF RISERS, TREADS, AND HEAD HEIGHT REQUIREMENTS. TREADS DEPTH TO BE 11" MIN AND RISER HEIGHT TO BE 7" MAX.
- EXTERIOR PATIO / SLAB PROVIDE 500S SACROFICIAL SLAB 4x6-3x MIN W/ BAR OR MESH REINFORCEMENT AS REQUIRED. INSTALL EXTERIOR PAVERS / TILE OVER SACROFICIAL SLAB. VERIFY W/ LANDSCAPE DRAWINGS & INTERIOR DESIGN PACKAGE FOR CONCRETE FINISH / PAVING / TILE SELECTION.
- SITE RETAINING WALL COORDINATE W/ CIVIL DRAWINGS & LANDSCAPE DRAWINGS FOR TOP AND BOTTOM OF RETAINING WALLS. RETAINING ARE TO FOLLOW THE LOCAL JURISDICTION RULE AND CODES.
- CANTILEVER STRUCTURE FLOOR (STEEL OR EXTENDED SLAB) SYSTEM. SEE STRUCTURAL DRAWINGS FOR LAYOUT, MEMBER SIZE AND REINFORCEMENT DETAILS.
- WALKWAY BRIDGE (STEEL STRUCTURE) SEE STRUCTURAL DRAWINGS FOR LAYOUT, MEMBER SIZE AND REINFORCEMENT DETAILS.
- DRIVEWAY SLAB (500S / ASPHALT) SLOPE DRIVEWAY AWAY FROM BUILDING / STRUCTURE. PROVIDE CURB & GUTTER WHERE REQUIRED. REFER TO CIVIL / LANDSCAPE DRAWINGS DETAILS AND DRAINAGE REQUIREMENTS. PROVIDE BAR OR MESH REINFORCEMENT AS REQUIRED.
- HOSE SPROUT(S) (BBS VERIFY LOCATIONS) PRIOR TO INSTALLATION. FREEZE LESS BACKFLOW PREVENTION REQUIRED AT ALL EXTERIOR LOCATIONS. PROVIDE 1" (1/2" MIN) AT ALL GARAGE LOCATIONS. VERIFY THESE SPROUT PRODUCT TYPE WITH ARCHITECTURAL SPECIFICATIONS.
- AIR CONDENSING - AC UNIT(S) (PAD AND/OR TRASH BIN) ENCLOSURE WALL(S). AC PAD IS TO BE 500S W/ PROVIDE BAR OR MESH REINFORCEMENT. CONTRACTOR TO USE OWN DISCRETION WHEN PLACING EXTERIOR EQUIPMENT (AC UNIT(S), HEATING, AND ANY OTHER EQUIPMENT FOR ENCLOSURE WALL DETAILS. SEE 10A100).
- PROPOSED LOCATION OF THE UTILITY METERS (IE WATER, POWER, GAS, EXT.) CONTRACTOR TO USE OWN DISCRETION WHEN PLACING EXTERIOR EQUIPMENT (AC UNIT(S), HEATING, AND ANY OTHER EQUIPMENT) EQUIPMENT IS TO BE PLACED OUT OF THE LINE OF SIGHT. SCHEDULING SHALL HAVE NO CLEAR GAP WIDER THAN 4" AND SHALL MEET CURRENT RC REQUIREMENTS. VERIFY HANGING AND / OR CHANGERS IN THE DESIGNER AND OWNER ON THE PROFILE AND COLOR PRIOR TO ORDERING AND INSTALLATION.
- OUTDOOR GAS FIREPLACE / PIT. PROVIDE A GAS PRE-BUILT FIRE PLACE. PROVIDE GAS SHUT OFF VALVE AT EACH FIREPLACE LOCATIONS. PROVIDE ALL REQUIRED PREHEATING, VENTS AND / OR FUELS INSTALLED PER MANUF. RECOMMENDATIONS.
- EXTERIOR COLUMNS (POST AND DECORATIVE BEAM (ABOVE)) SEE STRUCTURAL DRAWINGS FOR MEMBER SIZE, REINFORCEMENT AND ATTACHMENT REQUIREMENTS.
- WATER FEATURE / WATERFALL. REFER TO LANDSCAPE DRAWINGS FOR DETAILS AND SEALANT REQUIREMENTS. PROVIDE ADDITIONAL CONDUIT W/ LOW VOLTAGE WIRE TO ALLOW FOR ON/OFF ACCESS FROM WITH-IN HOME INTERIOR.
- POOL / SPA REFER TO LANDSCAPE DRAWINGS FOR DETAILS AND SEALANT REQUIREMENTS. PROVIDE ADDITIONAL CONDUIT W/ LOW VOLTAGE WIRE TO ALLOW FOR ON/OFF ACCESS FROM WITH-IN HOME INTERIOR.
- SPIRAL STAIRCASE (POWER COATED STEEL) FIELD VERIFY FOR AMOUNT OF RISERS, TREADS, AND HEAD HEIGHT REQUIREMENTS. TREAD DEPTH TO BE 11" MIN AND RISER HEIGHT TO BE 7" MIN. PROVIDE HANDRAIL & GUARDRAIL SHALL BE 36" MIN HIGH FROM TOP OF TREAD. BALUSTER SPACING SHALL HAVE NO CLEAR GAP WIDER THAN 4" AND SHALL MEET CURRENT RC REQUIREMENTS. VERIFY HANGING AND / OR CHANGERS IN THE DESIGNER AND OWNER ON THE PROFILE AND COLOR PRIOR TO ORDERING AND INSTALLATION.
- GARAGE SLAB (500S) SLOPE CONCRETE SLAB TO THE EXTERIOR OF GARAGE DOOR(S) AND DRIVEWAY. IF GARAGE FLOOR DRAIN ARE PROVIDED. SLOPE TO DRAIN. PROVIDE BAR OR MESH REINFORCEMENT AS REQUIRED. VERIFY W/ INTERIOR DESIGN PACKAGE FOR CONCRETE FINISH COATING SELECTION.
- GARAGE OVERHEAD DOOR (SIDE MOUNTED OPTION) FIELD VERIFY FOR GARAGE DOOR(S) ROUGH OPENING PRIOR TO ORDERING AND INSTALLATION. SEE DOOR SCHEDULE FOR TYPE, STYLE, AND OPERATION. PROVIDE POWER RECEPTACLE AT OPERATOR MOTOR.
- GARAGE WALLS & CEILING GYP BOARD IS TO RUN FROM FOUNDATION TO CEILING. PROVIDE ON THE GARAGE SIDE WALLS & CEILING. SINGLE LAYER 5/8" TYPE "X" GYP BOARD (1/4" RATED) ALL PENETRATIONS (PLUMBING, WATER, VACUUM, ETC.) THROUGH GARAGE FLOOR WALL TO BE METAL FINISH W/ FIRE RATING. (ALTERNATE SYSTEM: (2) LAYERS OF 1/2" TYPE "X" GYP BOARD).
- WATER HEATER (TANK OR ON DEMAND) PROVIDE DESIGNER AND/OR SCHEDULING. STRAITS TO OVERHEAD WATER HEATER INTO 1/2" PORTIONS. PROVIDE EXTERIOR RAIN WATER DRAIN. PROVIDE 1" (1/2" MIN) AT ALL GARAGE LOCATIONS. VERIFY W/ INTERIOR DESIGN PACKAGE FOR BASE HEIGHT OF WASHER & DRYER. WHERE REQUIRED PROVIDE FLOOR DRAIN AND / OR PAN AT ALL WASHER LOCATIONS).
- ELECTRICAL AND LOW VOLTAGE PANEL(S) PROPOSED LOCATION ELECTRICAL BREAKER PANEL AND / OR LOW VOLTAGE RACK. CONTRACTOR TO VERIFY BEST LOCATION W/ OWNER AND DESIGN TEAM AND SUBCONTRACTOR.
- FURNACE AND / OR FORCES AIR SYSTEM. PROPOSED LOCATION AND AMOUNT OF FURNACE UNIT(S). CONTRACTOR TO VERIFY LOCATION W/ DESIGN TEAM. PROVIDE ZONES SYSTEM AND REVIEW DUCT RUNS AND GRILL LOCATIONS) W/ OWNER AND DESIGN TEAM. OWNER TO DETERMINE AMOUNT OF HEATING / COOLING ZONES. SEE DETAIL 10A100.
- THERMOSTAT(S) PROPOSED LOCATION OF THERMOSTAT(S) PROPOSED LOCATION VERIFY LOCATION W/ DESIGN TEAM.
- FLOOR PLUG AND / OR RECEPTACLE VERIFY W/ ELECTRICAL LIGHT DRAWINGS FOR LOCATION(S). PROVIDE ANY REQUIREMENTS TO ACCOUNT FOR PLUG IN FLOOR 500S.
- GAS FIREPLACE. PROVIDE A GAS PRE-BUILT FIRE PLACE. PROVIDE GAS SHUT OFF VALVE AT EACH FIREPLACE LOCATIONS. PROVIDE ALL REQUIRED PREHEATING, VENTS AND / OR FUELS INSTALLED PER MANUF. RECOMMENDATIONS.
- FIREPLACE SURROUNDINGS, MANTEL, AND / OR HEARTH VERIFY W/ INTERIOR DESIGN PACKAGE FOR DESIGN ELEMENTS AND MATERIALS.
- FLOOR DRAIN RECESSSES THE FLOOR SYSTEM (500S) FLOOR SYSTEM TO ACCOUNT FOR FALL OF THE SLOPE TO THE DRAIN. SLOPE FINISH FLOOR MATERIAL TO DRAIN FLOOR DRAIN TO CONNECT INTO SEWER AND / OR STORM DRAIN SYSTEM.
- WASHER & DRYER. PROVIDE MANUFACTURE REQUIRED POWER AND GAS LINE SYSTEM TO EACH PAIR LOCATIONS. AFTER PLUG IN BE SELECTED BY OWNER. PROVIDE 1" (1/2" MIN) AT ALL GARAGE LOCATIONS. VERIFY W/ INTERIOR DESIGN PACKAGE FOR BASE HEIGHT OF WASHER & DRYER. WHERE REQUIRED PROVIDE FLOOR DRAIN AND / OR PAN AT ALL WASHER LOCATIONS).
- DRYER VENT & DUCTING. PROVIDE IN WALL RECESSSED WALL HOOKUP W/ 5" VENT DUCT FOR THE DRYER VENT TO OUTSIDE.
- ACCENT WALL(S) AND / OR ALCOVE. VERIFY ALL DETAILS, MATERIAL, RETURN AND ETC W/ INTERIOR DESIGN PACKAGE AND DESIGN TEAM.
- MATERIAL FACADE VERIFY ALL DETAILS, MATERIAL, RETURN AND ETC W/ INTERIOR DESIGN PACKAGE AND DESIGN TEAM.
- SOELEDGE DOOR. SEE DOOR SCHEDULE FOR TYPE, STYLE, AND OPERATION. PROVIDE AND INSTALL ALL REQUIRED SEALANT, FLASHING, AND THRESHOLDS AS PER MANUF. RECOMMENDATIONS.
- TYPICAL DOOR SPACING. PROVIDE ALL DOORS TO BE SPACED OFF OF THE WALL 5/8" OR PER DETAIL 10A100, UNLESS OTHER WISE NOTED OR DIMENSIONED.
- DOOR THRESHOLDS. TO VARY FROM LOCATION TO LOCATION. SEE DETAILS 8 & 11-12A100.
- SOELEDGE WINDOW AND / OR BUTTED GLASS SYSTEM. SEE WINDOW SCHEDULE FOR STYLE, AND OPERATION. VERIFY W/ THE EXTERIOR ELEVATION FOR THE SILL HEIGHT. PROVIDE AND INSTALL ALL REQUIRED SEALANT AND FLASHING AS PER MANUF. RECOMMENDATION.
- HIGH WINDOW AND / OR TRANSOM. TRANSOM AND / OR HIGH SILL WINDOW. SEE WINDOW SCHEDULE FOR STYLE, AND OPERATION. VERIFY W/ THE EXTERIOR ELEVATION FOR THE SILL HEIGHT.
- SKYLIGHT WINDOW. SEE WINDOW SCHEDULE FOR STYLE, AND OPERATION. PROVIDE SKYLIGHT ROOF CARD DETAIL SEE 71A100S.
- SINK BASIN. VERIFY W/ INTERIOR DESIGN PACKAGE FOR FUTURE SELECTIONS. PROVIDE DISPOSAL AT SINK W/ REQUIRED (GFCI) POWER RECEPTACLE.
- DISHWASHER. PROVIDE POWER RECEPTACLE (GFCI) AT EACH LOCATION. DISHWASHER TO OWNER SELECTED PRIOR TO ORDERING. VERIFY W/ INTERIOR DESIGN PACKAGE FOR ANY APPLIANCE REQUIREMENTS.
- REFRIGERATOR & FREEZER. VERIFY W/ OWNER PRIOR TO ORDERING APPLIANCE. CONTRACTOR TO VERIFY CABINETS THAT APPLIANCE WILL FIT IN DESIRED SPACE. PROVIDE MANUFACTURE REQUIRED POWER AND / OR WATER SYSTEM TO EACH LOCATION(S). VERIFY W/ INTERIOR DESIGN PACKAGE FOR ANY APPLIANCE REQUIREMENTS.
- APPLIANCE(S). VERIFY W/ OWNER PRIOR TO ORDERING APPLIANCE. CONTRACTOR TO VERIFY CABINETS THAT APPLIANCE WILL FIT IN DESIRED SPACE. PROVIDE MANUFACTURE REQUIRED WATER, SPLY, POWER AND / OR GAS SYSTEM TO EACH LOCATION(S).
- RANGE & STOVE / COOK TOP / WALL OVEN. PROVIDE REQUIRED BOTH REQUIRED POWER AND GAS LINE AT EACH LOCATION(S). APPLIANCE TO BE SELECTED BY OWNER. PROVIDE MANUFACTURE REQUIRED POWER AND GAS LINE SYSTEM TO EACH LOCATION(S). VERIFY W/ INTERIOR DESIGN PACKAGE FOR ANY APPLIANCE REQUIREMENTS.
- EXHAUST HOOD. PROVIDE HOOD ABOVE RANGE / COOKTOP. HOOD TO BE OWNER SELECTED PRIOR TO INSTALLATION. VERIFY W/ INTERIOR DESIGN PACKAGE FOR HOOD FINISH MATERIAL.
- OUTDOOR GRILL / KITCHENETTE. PROVIDE STUBBED GAS LINE TO OUTDOOR KITCHEN AREA. PROVIDE GAS SHUT OFF VALVE. VERIFY W/ INTERIOR DESIGN PACKAGE FOR KITCHEN LAYOUT AND REQUIREMENTS.
- OUTDOOR MISTERS (ABOVE) PROVIDE ALL REQUIRED WATERPROOFING MEASURE TO ALLOW CEILING MISTERS. FOR CEILING MISTERS SEE 10A100.
- OVERHEAD HEATERS. PROVIDE GAS HEATERS. LOCATE HEATER CONTROLS ON A WALL NEAR LOCATION 3/8" AFF. INSTALL PER MANUF. RECOMMENDATIONS. PROVIDE GAS SHUT OFF VALVE AT EACH LOCATION.
- BUILT-IN ISLAND(S). PROVIDE ROUGH-IN POWER SUPPLY AT ALL LOCATIONS. VERIFY ALL ISLAND DETAILS W/ INTERIOR DESIGN PACKAGE.
- MILLWORK / CABINETS (BASE & UPPER & FULL HEIGHT & MANTLES) VERIFY ALL CABINETS ELEVATIONS W/ INTERIOR DESIGN PACKAGE. PROVIDE ALL DRAWERS AND DOORS W/ SOFT CLOSERS.
- BUILT-IN MILLWORK (CABINETS, LOCKERS, ETC.) VERIFY ALL CABINETS ELEVATION W/ INTERIOR DESIGN PACKAGE. PROVIDE ALL DRAWERS AND DOORS W/ SOFT CLOSERS.
- BUILT-IN MILLWORK (SHELVES, BENCHES) VERIFY ALL CABINETS ELEVATIONS W/ INTERIOR DESIGN PACKAGE. BUILT-IN MILLWORK (SHELVES) VERIFY ALL CABINETS ELEVATIONS W/ INTERIOR DESIGN PACKAGE.
- GARAGE CABINETS (CABINETS, LOCKERS, ETC.) TO BE DESIGNED BY OTHERS. VERIFY ALL CABINETS ELEVATION W/ INTERIOR DESIGN PACKAGE. PROVIDE ALL DRAWERS AND DOORS TO BE SOFT CLOSERS.
- CLOSET CUSTOM AND / OR SHELVING & ROD TO BE DESIGNED BY OTHERS. CONTRACTOR DESIGN AND STYLE W/ DESIGN TEAM AND INTERIOR DESIGN PACKAGE FOR AND REQUIREMENTS.
- FREE STANDING TUB. PROVIDE AND INSTALLER TUB PER MANUF. RECOMMENDATION. VERIFY W/ INTERIOR PACKAGE FOR LOCATION. THE WATER SHOUT. VERIFY DRAIN LOCATION W/ PRODUCT AND PROVIDE CONCRETE DOWN OUT FOR TUB DRAIN.
- VESTAL SINK. COORDINATE THE PLUMBING DRAINS TO ACCOUNT FOR HEIGHT OF DRAIN. VERIFY W/ INTERIOR DESIGN PACKAGE PRIOR TO ORDERING PRODUCT.
- SHOWER DRAIN (LINEAR / SQUARE) COORDINATE ROUGH-IN LOCATION OF FLOOR DRAIN PRIOR TO INSTALLING. COORDINATE HEIGHT OF DRAIN FOR SELECTED TILE DEPTH PRODUCT AT EACH LOCATION(S). SLOPE FLOOR / TILE TO DRAIN. SEE DETAILS 2A100.
- SHOWER GLASS PARTITION W/ DOOR. PROVIDE TEMPERED SHOWER GLASS & DOOR. VERIFY W/ INTERIOR PACKAGE AND OWNER FOR SELECTION OF OPAQUE DENSITY TYPE AND HARDWARE.
- PROVIDE TILED SHOWER NICHES SHELF AND / OR SHOWER BENCH (WHERE OCCUR) VERIFY W/ INTERIOR DESIGN PACKAGE FOR TILE / BENCH MATERIAL AND LAYOUT.
- NOT USED.
- GUARDRAIL SHALL BE 36" MIN HIGH FROM TOP OF TREAD. BALUSTER SPACING SHALL HAVE NO CLEAR GAP WIDER THAN 4" AND SHALL MEET CURRENT RC REQUIREMENTS. VERIFY HANGING AND / OR CHANGERS IN THE DESIGNER AND OWNER ON THE PROFILE AND COLOR PRIOR TO ORDERING AND INSTALLATION.
- SAFETY TIE-OFF. PROVIDE RECESS IN CONCRETE SAFETY TIE OFF POINT. INSTALL PER MANUFACTURE RECOMMENDATIONS.
- CEILING OR BUILDING ABOVE. THE LINE REPRESENT THE CHANGE IN THE CEILING HEIGHTS AND / OR PRESENCES OF AN STRUCTURE SYSTEMS ABOVE.


THE BLACK DAHLIA
(NEW CONSTRUCTION CUSTOM HOME)
2387 SOUTH VILLAGE Dr. (LOT 2) SANTA CLARA, UT 84765
PREPARED FOR MR. & MRS. LETHIN (CLIENTS OF MARKAY JOHNSON CONST.)

PROJECT NUMBER : 25-01
DATE 21-Aug-2025

REVISION	DATE
0. ORIGINAL ISSUE	8.19.25
1.	
2.	
3.	


SHEET TITLE
MAIN Lvl
FLOOR PLAN

SHEET NUMBER
A.102
(24 x 36" ARCH D)

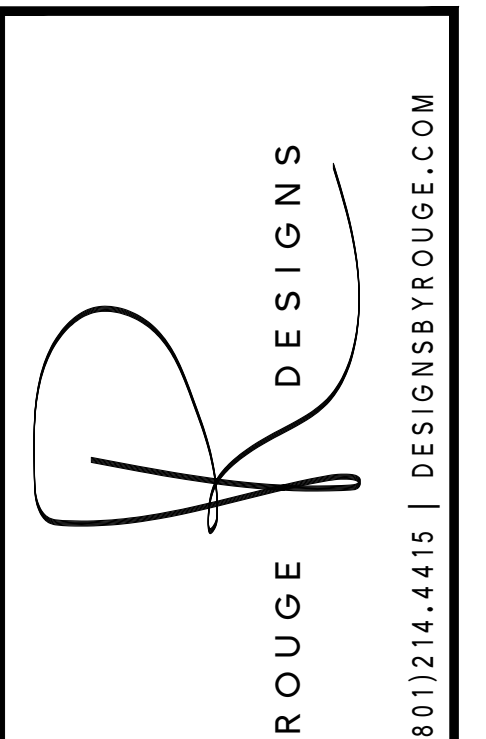


THESE PLANS MAY ONLY BE USED FOR THIS SPECIFIC ADDRESS AND PROJECT ONLY. THESE PLANS AND DOCUMENTS ARE THE INTELLECTUAL PROPERTY OF ROUGE DESIGNS LLC. ANY REUSE OR MODIFICATION OF THESE PLANS WITHOUT THE WRITTEN PERMISSION OF ROUGE DESIGNS LLC IS STRICTLY PROHIBITED. THESE PLANS ARE THE PROPERTY OF ROUGE DESIGNS LLC. ANY REUSE OR MODIFICATION OF THESE PLANS WITHOUT THE WRITTEN PERMISSION OF ROUGE DESIGNS LLC IS STRICTLY PROHIBITED.

THESE PLANS ARE INSTRUMENTS OF PROFESSIONAL SERVICE AND ARE THE INTELLECTUAL PROPERTY OF ROUGE DESIGNS LLC. AND ARE PROTECTED BY COMMON LAW, STATUTE, AND OTHER RESERVED RIGHTS INCLUDING, BUT NOT LIMITED TO, COPYRIGHT. THESE PLANS SHALL NOT BE REPRODUCED OR USED FOR ANY OTHER PROJECT, WITHOUT THE WRITTEN CONSENT OF ROUGE DESIGNS LLC. THE PREPARE OF THESE PLANS ASSUMES NO FINANCIAL LIABILITY RESULTING FROM ERRORS OR OMISSIONS IN THESE PLANS.

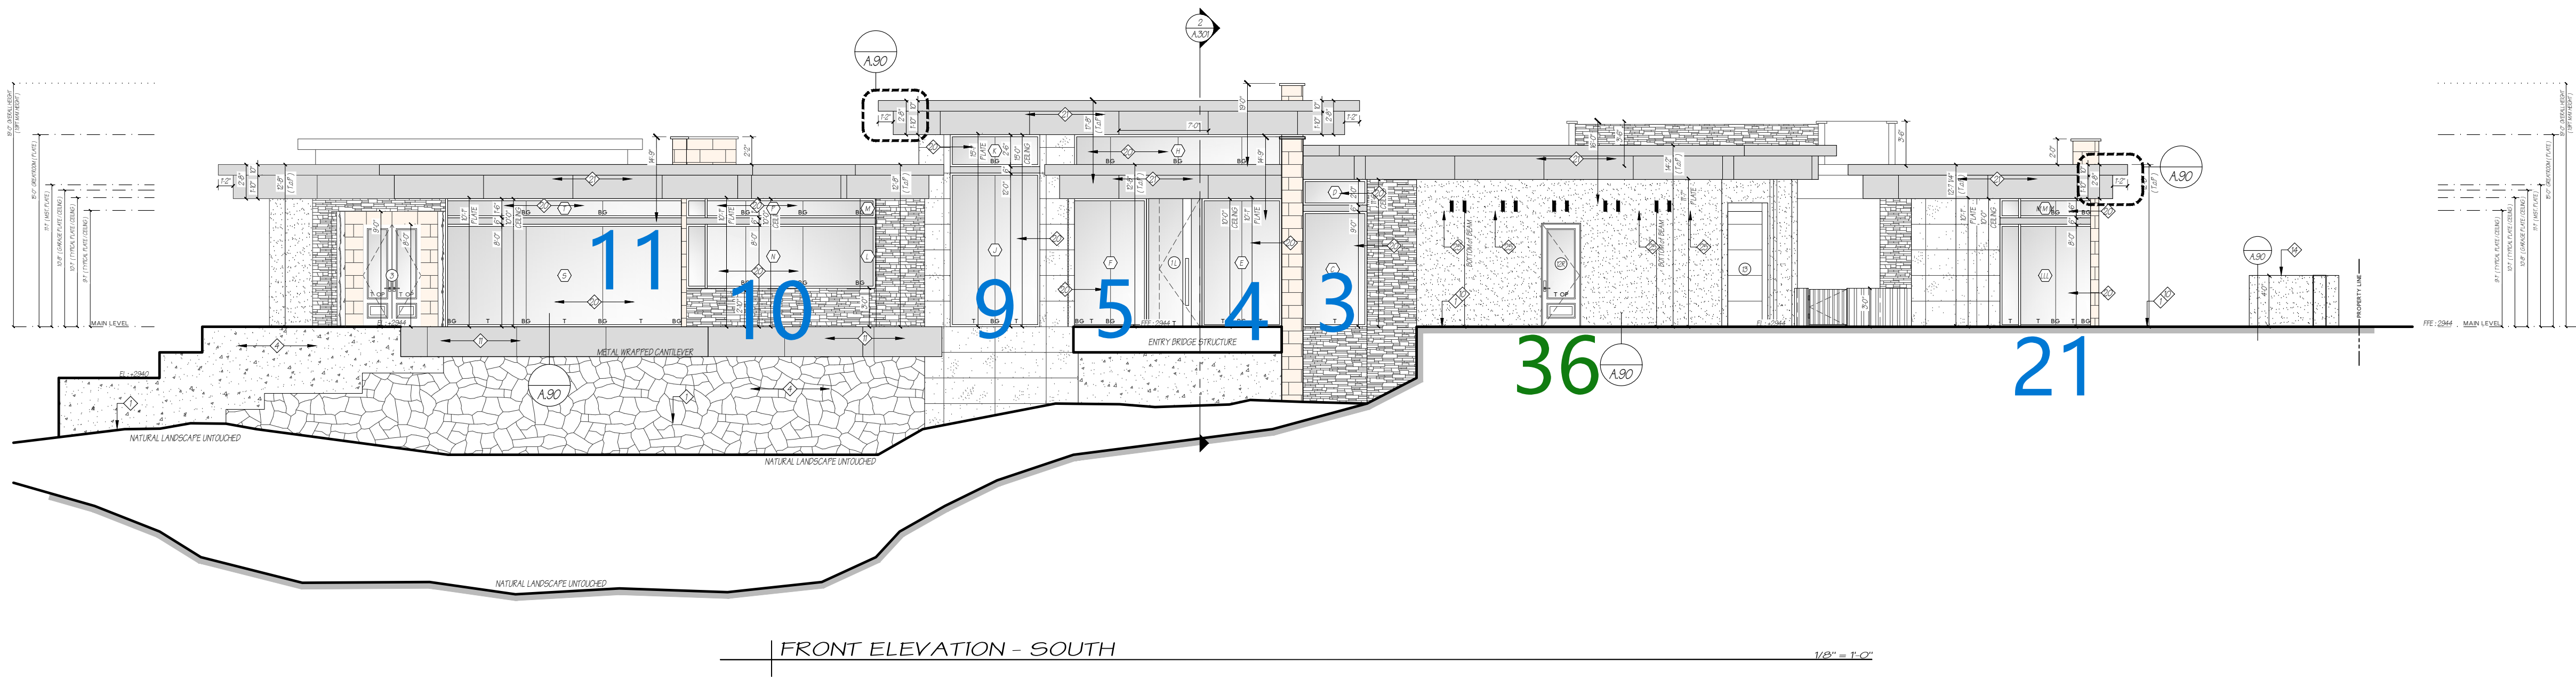


FRONT ELEVATION - SOUTH

1/8" = 1'-0"

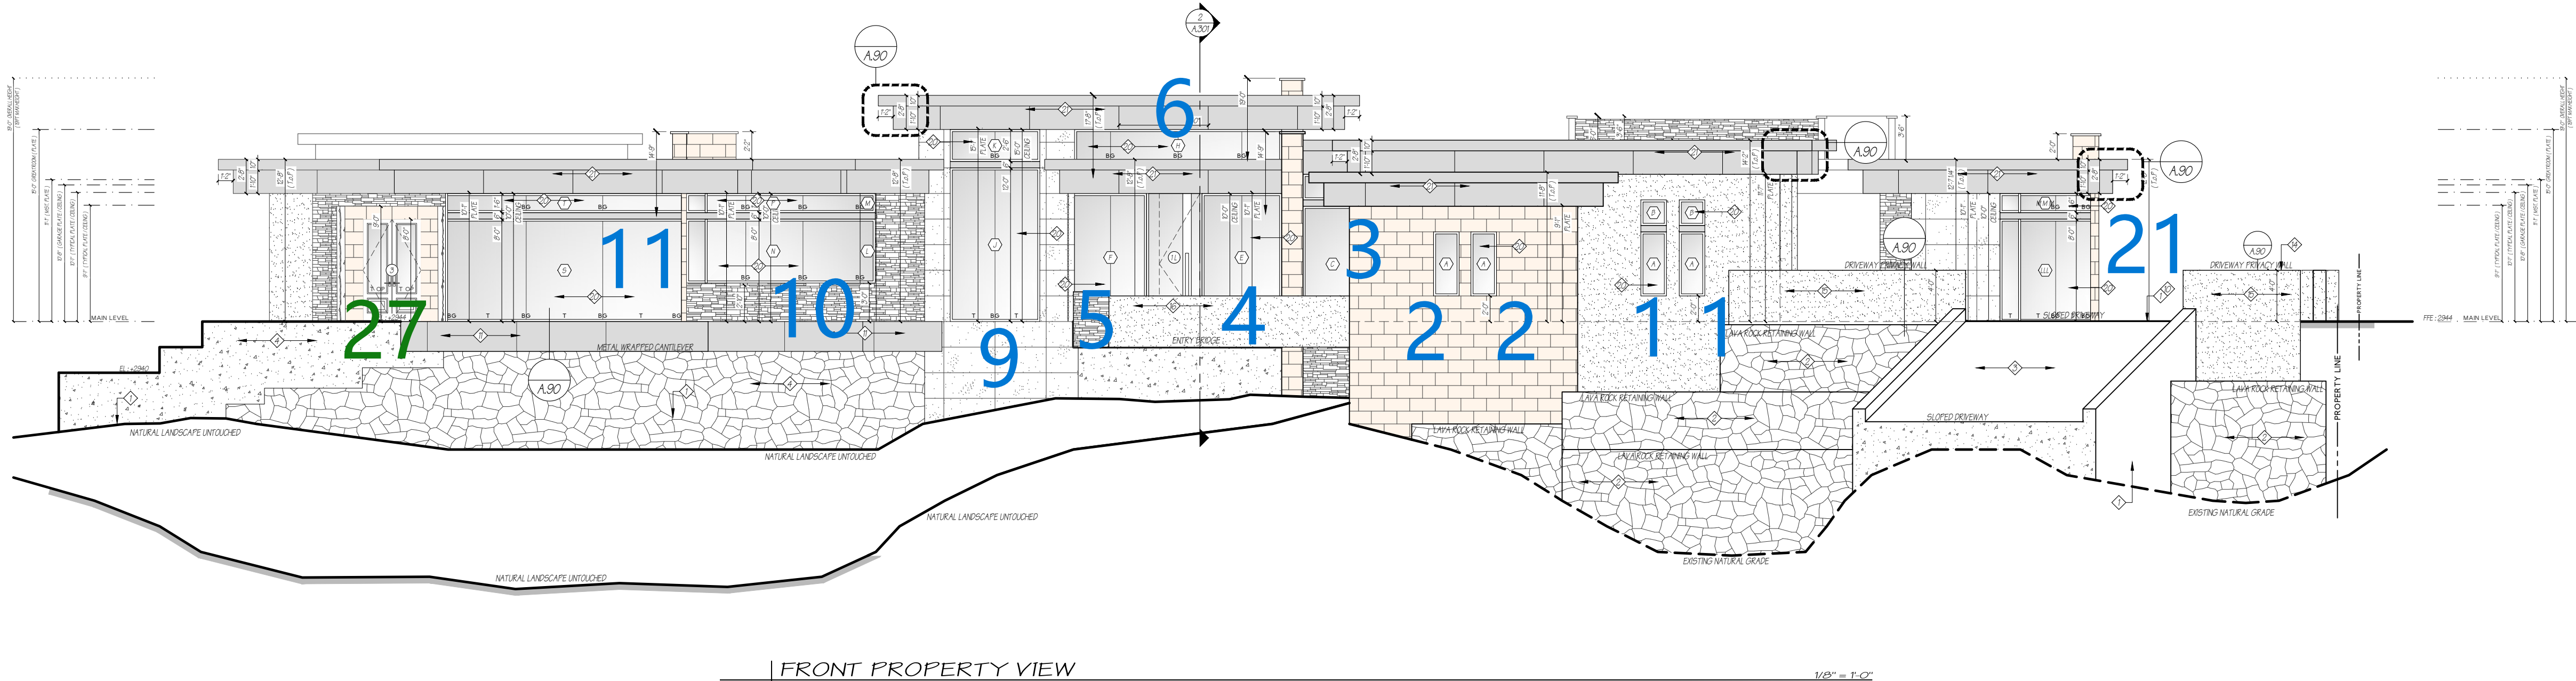

FRONT PROPERTY VIEW

1/8" = 1'-0"

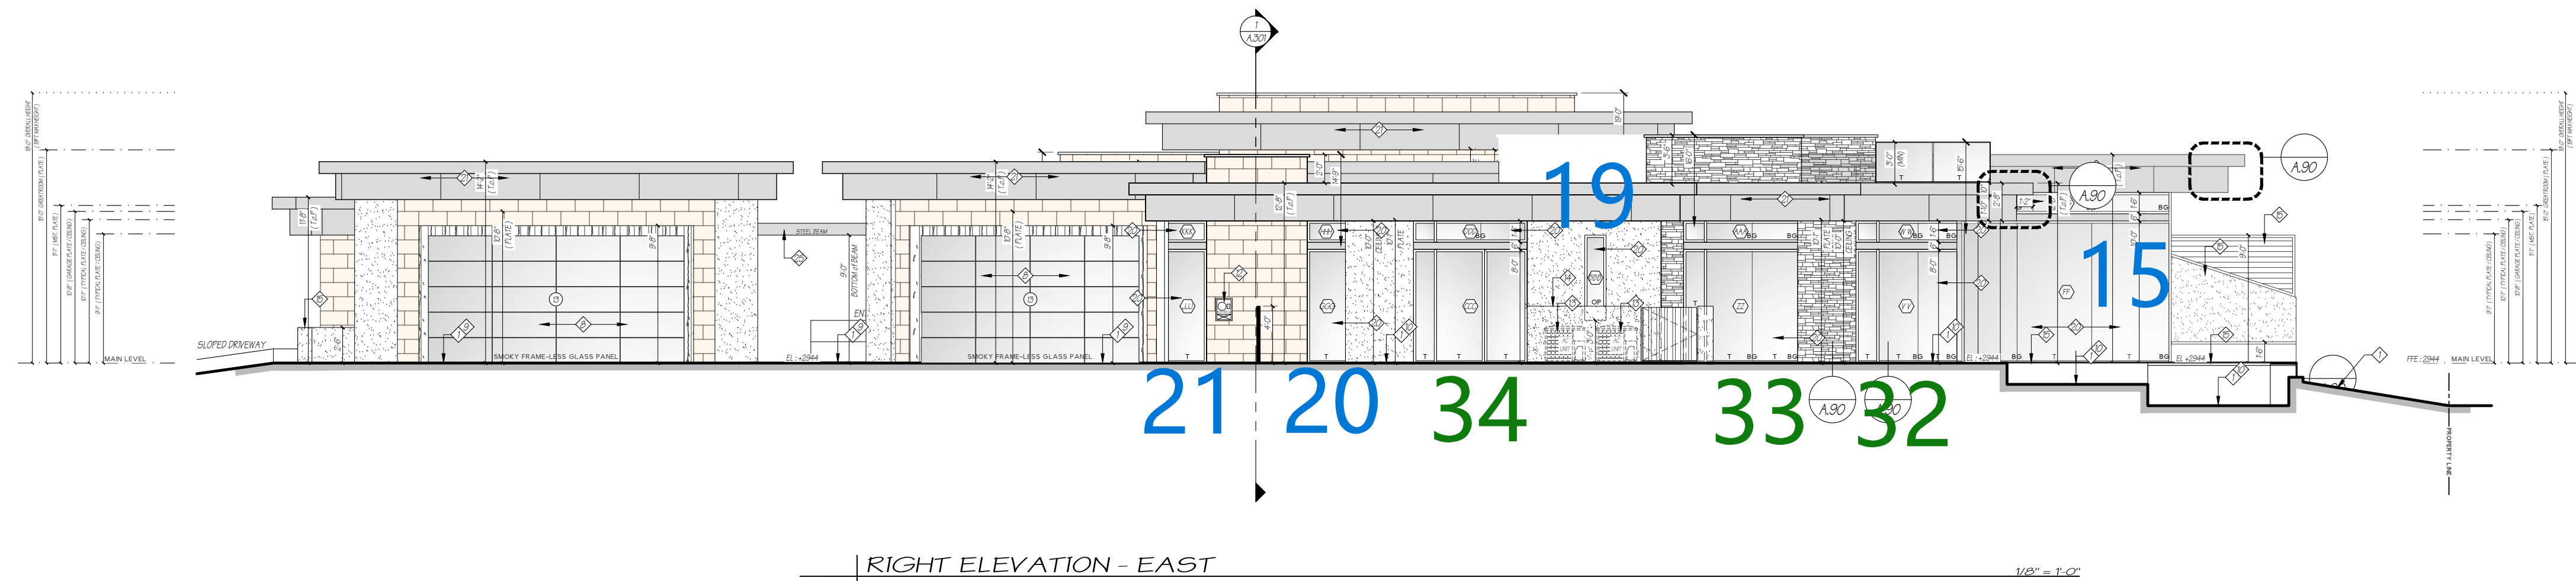

RIGHT ELEVATION - EAST

1/8" = 1'-0"

ELEVATION MATERIAL LEGEND:

	CLUSTERED / NATURAL STONE VENEER (TOTAL SQFT: ~ 000) COLOR: (REFER TO EXTERIOR SELECTION SHEET)
	NATURAL STONE TILE (TOTAL SQFT: ~ 000) COLOR: (REFER TO EXTERIOR SELECTION SHEET)
	LIGHT WEIGHT CONCRETE TILE VENEER (TOTAL SQFT: ~ 000) COLOR: (REFER TO EXTERIOR SELECTION SHEET)
	STUCCO HARD COAT (ULTRA SMOOTH / SHINY TEXTURE) (TOTAL SQFT: ~ 000) COLOR: (REFER TO EXTERIOR SELECTION SHEET)
	STEPPED METAL FASCIA / DRIP EDGE (SOLID) METAL FASCIA (TOTAL SQFT: ~ 000) COLOR: (REFER TO EXTERIOR SELECTION SHEET)
	WOODEN EXTERIOR CLADDING (TOTAL SQFT: ~ 000) COLOR: (REFER TO EXTERIOR SELECTION SHEET)
	LAVA ROCK VENEER OR BOULDER LAVA ROCK (TOTAL SQFT: ~ 000) COLOR: (REFER TO EXTERIOR SELECTION SHEET)

GARAGE DOORS COLOR: _____ MANUF. STANDARD BRONZE
EXTERIOR WINDOW FRAME COLOR: _____ MANUF. STANDARD DARK BRONZE
EXTERIOR DOORS COLOR: _____ MANUF. STANDARD DARK BRONZE
SOPHIT: _____ REFER TO EXTERIOR SELECTION SHEET
PARAPET CAP: _____ REFER TO EXTERIOR SELECTION SHEET

** INSTALL MATERIAL TYPES PER MANUFACTURE RECOMMENDATIONS, ATTACH VENEER PER GENERAL STRUCTURAL NOTES, WHERE APPLIES PROVIDE AND INSTALL REQUIRED CONTROL JOINTS PER MANUF. **

EXTERIOR ELEVATION GENERAL NOTES :

- CONTRACTOR IS RESPONSIBLE FOR PREPARATION, WATERPROOFING, AND INSTALLATION OF CLADDING / RAIN SCREEN / STUCCO SCOTCH COAT / EIF ASSEMBLY PER MANUF. RECOMMENDATIONS. FILL ALL JOINTS WITH MATCHING CAULK.
- NO MECHANICAL EQUIPMENT, VENT STACKS, FASTENERS, SNOW INVERTER, FLUENCE FLUE, METAL WORK AND OTHER VISUAL ELEMENTS SHALL BE LOCATED ON THE FRONT OF THE HOME.
- INSTALL ALL EXTERIOR MATERIAL / CLADDING PER MANUF. RECOMMENDATIONS.
- ALL SEALANT / CAULKING SYSTEMS AND GASKETS AND WATERPROOFING MEMBRANE SHALL BE ASSEMBLED IN SUCH A MANNER TO PROVIDE A HIGH QUALITY WEATHERPROOFING BUILDING ENCLOSURE.
- ALL SEALANT / CAULKING COLOR SHALL MATCH THE ADJACENT MATERIAL OR OTHERWISE NOTED.
- ALL FASTENERS ARE TO BE CONCEALED, EXPECT AS SPECIFIED. ALL BUTT JOINTS ARE TO HAVE CONCEALED / PACKED UP TO 600 WITH CAPTIVE SEALANT.
- 10% OF THE FOUNDATION IS TO EXTEND ABOVE FINISH GRADE GIN (MIN).
- ALL FLASHING, VENTING AND PIPES ARE TO BE PAINTED TO MATCH ADJACENT MATERIALS.
- NO REFLECTIVE EXTERIOR MATERIAL ARE ALLOWED.
- PROVIDE OPAQUE GLAZING AT BATHROOM / WATERCLOSET LOCATION(S), VERIFY W/ INTERIOR DESIGN TEAM.
- EXTERIOR LIGHTING SHALL SHADOWED AND POSITIONED SO AS TO REFLECT LIGHT AWAY FROM ADJACENT RESIDENCE AND ROADWAYS.

ELEVATION HEIGHT NOTES :

- ARCHITECTURAL FOOTING AND FOUNDATION ELEVATION ARE RELATIVE TO ARCHITECTURAL MAIN FLOOR OF + 0'-0" ELEVATION.
- ARCHITECTURAL + 0'-0" ELEVATION = SURVEY / CIVIL ENGINEERING SITE PLAN "FF" FLOOR ELEVATION. COORDINATE WITH CIVIL DRAWINGS.

THE BLACK DAHLIA
(NEW CONSTRUCTION CUSTOM HOME)
2387 SOUTH VILLAGE Dr. (LOT 2) SANTA CLARA, UT 84765
PREPARED FOR MR. & MRS. LETHIN (CLIENTS OF MARKAY JOHNSON CONST.)

PROJECT NUMBER: 25-01

DATE
21-Aug-2025

#	REVISION	DATE
0.	ORIGINAL ISSUE	8.19.25
1.		
2.		
3.		

SHEET TITLE

EXTERIOR
ELEVATIONS

SHEET NUMBER

A.201


(24 x 36 : ARCH D)

PLANS PRINTED ON 11 x 17 PAPER ARE 1/2 THE SCALE NOTED

ROUGE
DESIGNS


THESE PLANS MAY ONLY BE USED FOR THIS SPECIFIC ADDRESS AND PROJECT ONLY. THESE PLANS AND DOCUMENTS ARE THE INTELLECTUAL PROPERTY OF ROUGE DESIGNS LLC, AND ANY REUSE OR FURTHER DISTRIBUTION THEREOF IN PART OR IN WHOLE WITHOUT THE WRITTEN PERMISSION OF ROUGE DESIGNS LLC IS STRICTLY PROHIBITED. THE DESIGN REPRESENTED BY THESE DRAWINGS IS SOLD TO THE CLIENT FOR A ONE TIME USE, UNLESS OTHERWISE AGREED UPON IN WRITING BY ARCHITECT OR ENGINEER. ROUGE DESIGNS LLC, THE DESIGNER IS NOT AN ARCHITECT OR ENGINEER.
© COPYRIGHT 2025 ROUGE DESIGNS LLC

THESE PLANS ARE INSTRUMENTS OF PROFESSIONAL SERVICE AND ARE THE INTELLECTUAL PROPERTY OF ROUGE DESIGNS LLC. ANY REUSE OR FURTHER DISTRIBUTION OF THESE PLANS WITHOUT THE WRITTEN CONSENT OF ROUGE DESIGNS LLC IS STRICTLY PROHIBITED. THESE PLANS SHALL NOT BE REPRODUCED OR USED FOR ANY OTHER PROJECT WITHOUT THE WRITTEN CONSENT OF ROUGE DESIGNS LLC. THE PREPARE OF THESE PLANS ASSUMES NO FINANCIAL LIABILITY RESULTING FROM ERRORS OR OMISSIONS IN THESE PLANS.

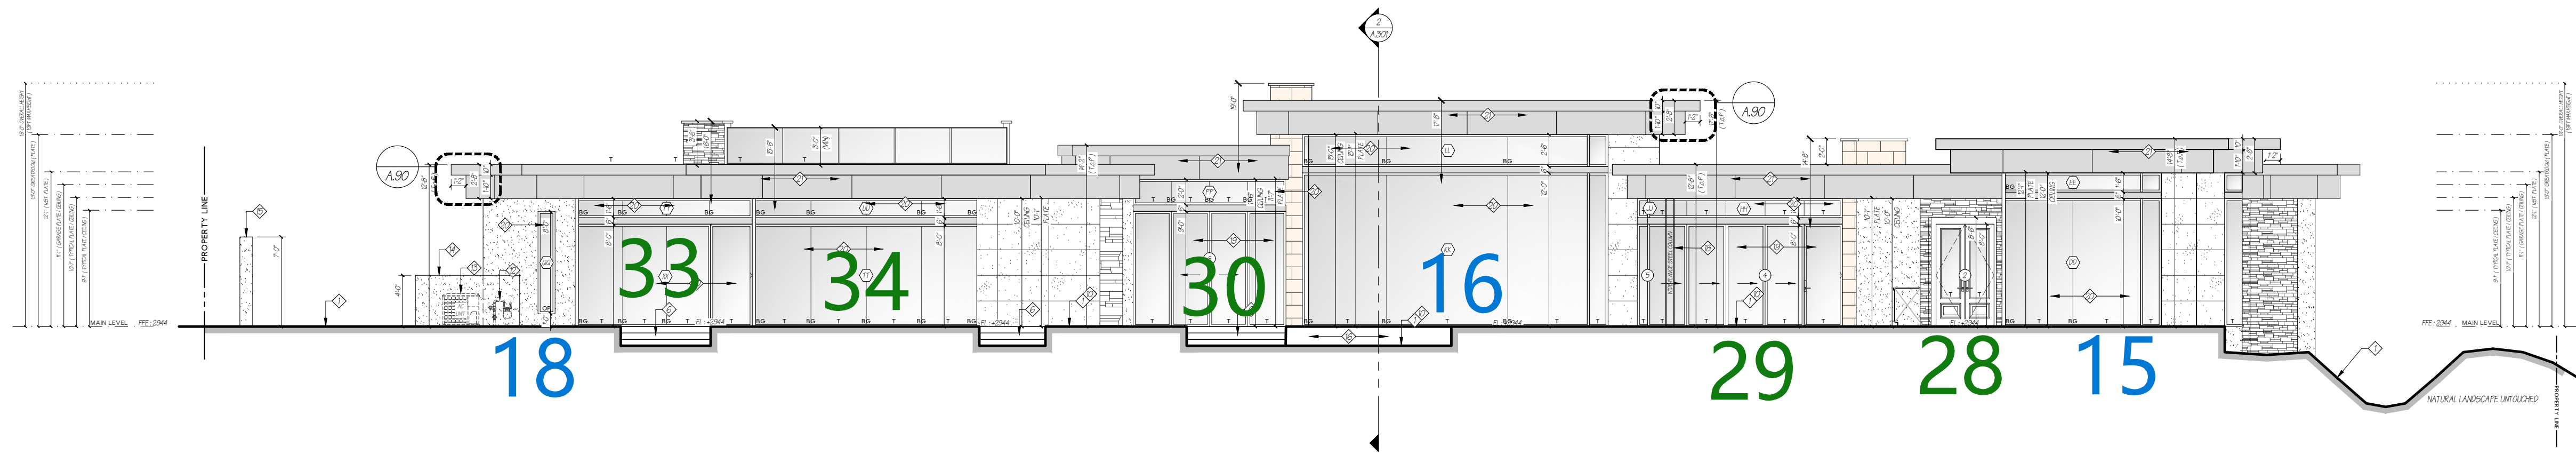


REAR ELEVATION - NORTH

1/8" = 1'-0"

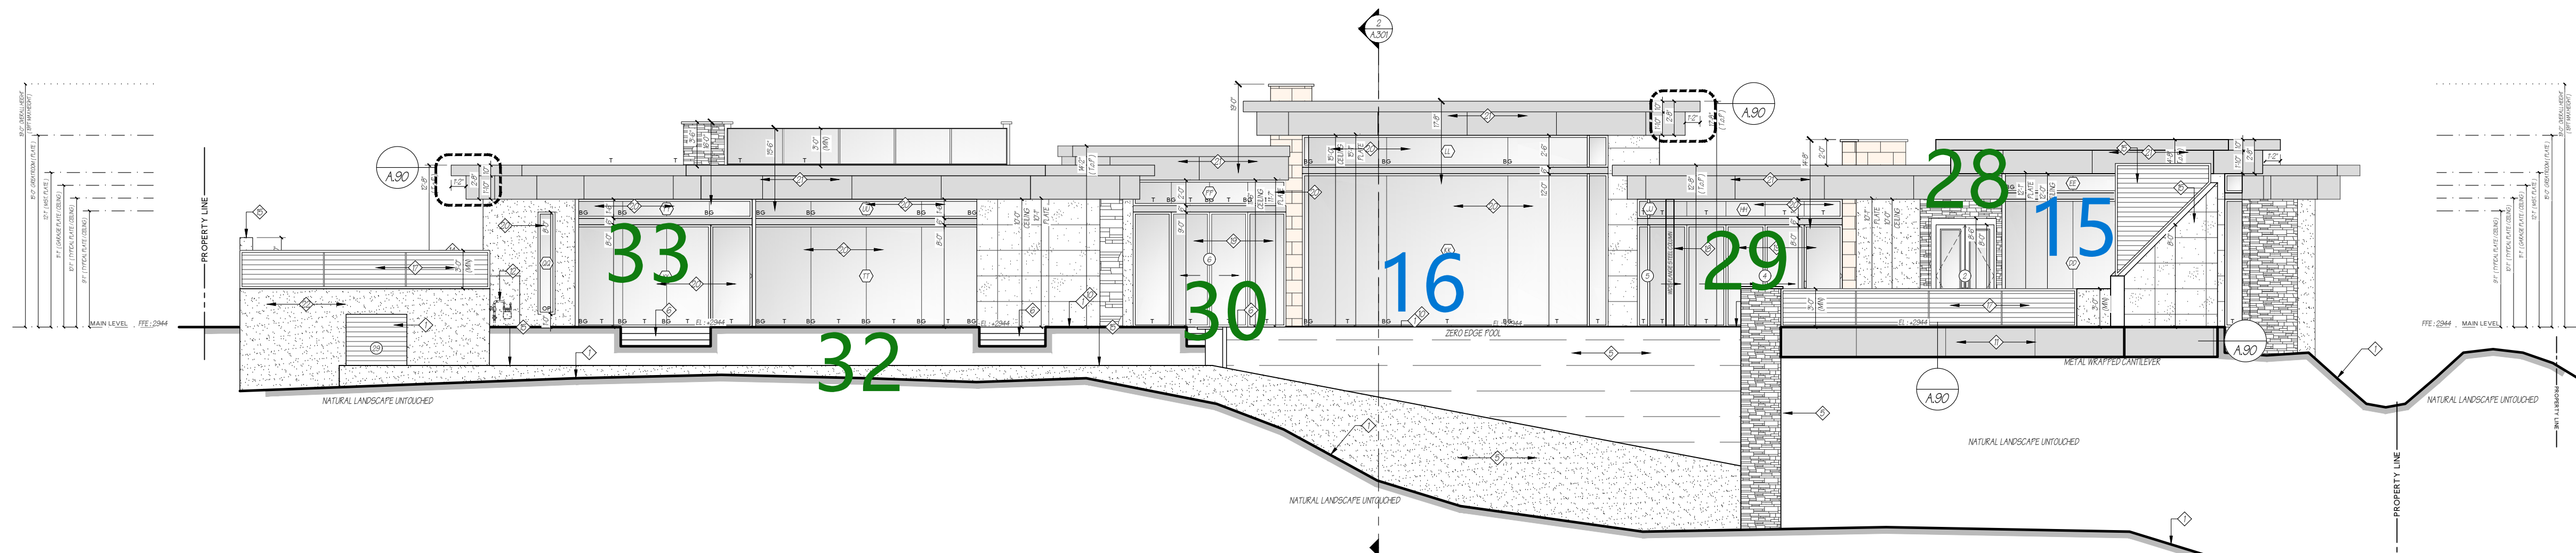

REAR PROPERTY ELEVATION

1/8" = 1'-0"

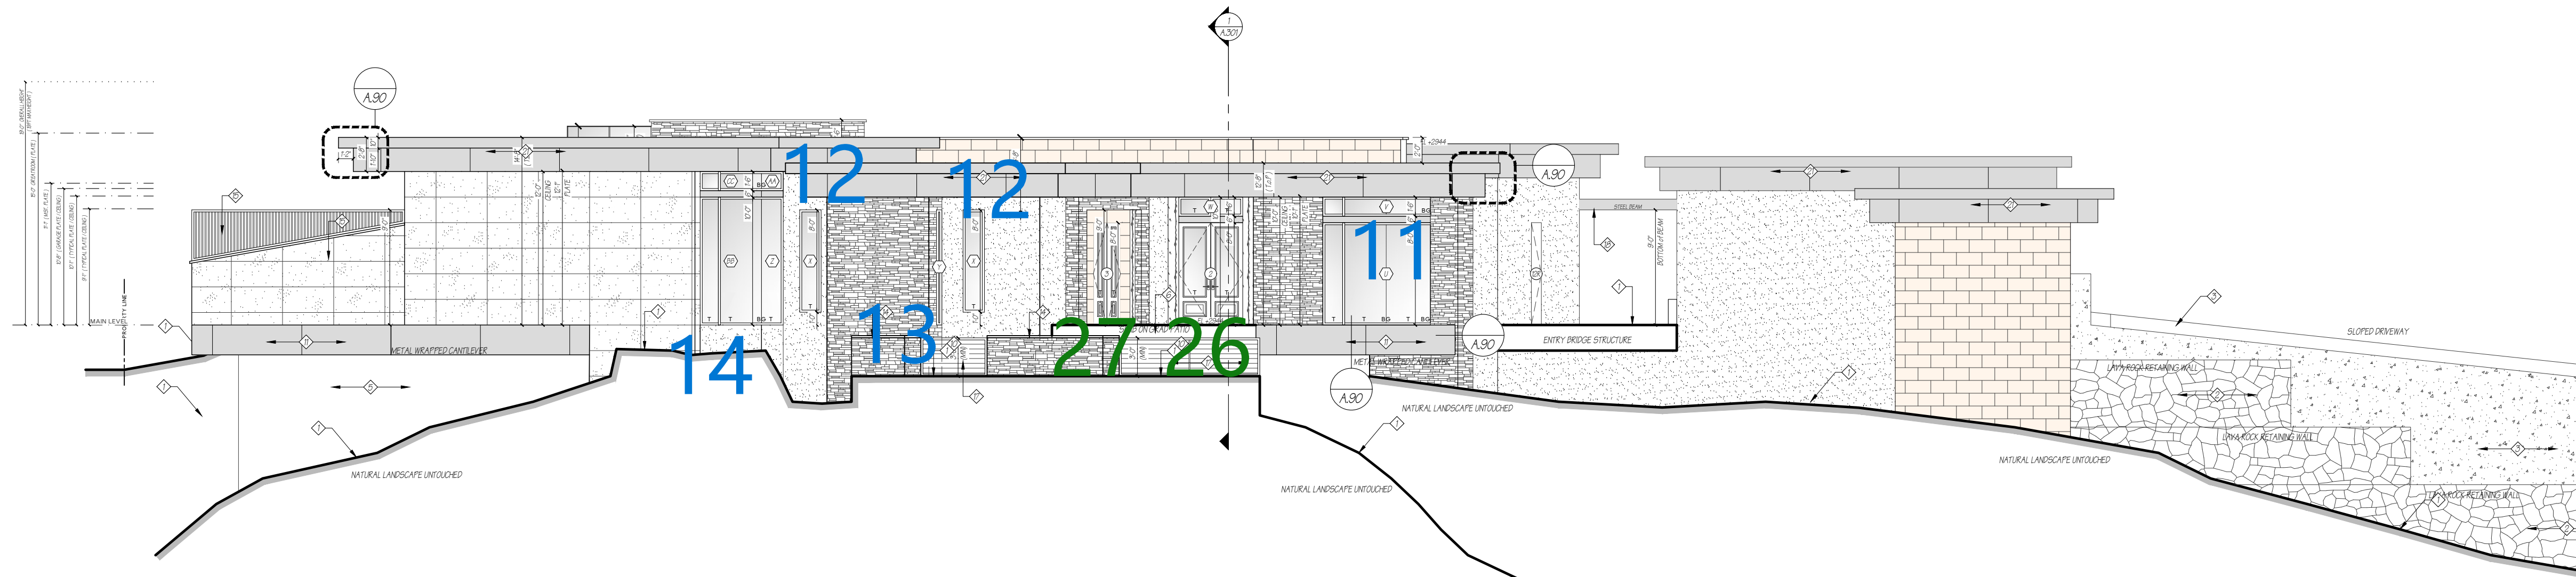

LEFT ELEVATION - WEST

1/8" = 1'-0"

ELEVATION MATERIAL LEGEND:	
	CLUSTERED / NATURAL STONE VENEER (TOTAL SQFT: ~ 000)
	NATURAL STONE TILE (TOTAL SQFT: ~ 000)
	LIGHT WEIGHT CONCRETE TILE VENEER (TOTAL SQFT: ~ 000)
	STUCCO HARD COAT (ULTRA SMOOTH / SHINY TEXTURE) (TOTAL SQFT: ~ 000)
	STEPPED METAL FASCIA / DRIP EDGE (SOLID) (TOTAL SQFT: ~ 000)
	METAL FASCIA (TOTAL SQFT: ~ 000)
	WOODEN EXTERIOR CLADDING (TOTAL SQFT: ~ 000)
	LAVA ROCK VENEER OR BOULDER LAVA ROCK (TOTAL SQFT: ~ 000)
GARAGE DOORS COLOR: _____ MANUF. STANDARD BRONZE	
EXTERIOR WINDOW FRAME COLOR: _____ MANUF. STANDARD DARK BRONZE	
EXTERIOR DOORS COLOR: _____ MANUF. STANDARD DARK BRONZE	
SOPHIT: _____ REFER TO EXTERIOR SELECTION SHEET	
PARAPET CAP: _____ REFER TO EXTERIOR SELECTION SHEET	

** INSTALL MATERIAL TYPES PER MANUFACTURE RECOMMENDATIONS. ATTACH VENEER PER GENERAL STRUCTURAL NOTES, WHERE APPLIES PROVIDE AND INSTALL REQUIRED CONTROL JOINTS PER MANUF. **

EXTERIOR ELEVATION GENERAL NOTES:	
* CONTRACTOR IS RESPONSIBLE FOR PREPARATION, WATERPROOFING, AND INSTALLATION OF CLADDING / RAIN SCREEN / STUCCO SCRATCH COAT / EIF ASSEMBLY PER MANUF. RECOMMENDATIONS. FILL ALL JOINTS WITH MATCHING CAULK.	
* NO MECHANICAL EQUIPMENT, VENT STACKS, FASTENERS, SNOW DIVERTER, FLUENCE FLUE, METAL WORK AND OTHER VISUAL ELEMENTS SHALL BE LOCATED ON THE FRONT OF THE HOME.	
* INSTALL ALL EXTERIOR MATERIAL / CLADDING PER MANUF. RECOMMENDATIONS.	
* ALL SEALANT / FLASHING SYSTEMS AND GASKETS AND WATERPROOFING MEMBRANE SHALL BE ASSEMBLED IN SUCH A MANNER TO PROVIDE A HIGH QUALITY WEATHERPROOFING BUILDING ENCLOSURE.	
* ALL SEALANT / CAULKING COLOR SHALL MATCH THE ADJACENT MATERIAL OR OTHERWISE NOTED.	
* ALL FASTENERS ARE TO BE CONCEALED, EXPECT AS SPECIFIED. ALL BUTT JOINTS ARE TO HAVE CONCEALED / PACKED UP TO 800 WITH CAPTIVE SEALANT.	
* TOP OF THE FOUNDATION IS TO EXTEND ABOVE FINISH GRADE 6IN (MIN).	
* ALL FLASHING, VENTING AND PIPES ARE TO BE PAINTED TO MATCH ADJACENT MATERIALS.	
* NO REFLECTIVE EXTERIOR MATERIAL ARE ALLOWED.	
* PROVIDE OPAQUE GLAZING AT BATHROOM / WATERCLOSET LOCATION(S). VERIFY W/ INTERIOR DESIGN TEAM.	
* EXTERIOR LIGHTING SHALL SHADOWED AND POSITIONED SO AS TO REFLECT LIGHT AWAY FROM ADJACENT RESIDENCE AND ROADWAYS.	
ELEVATION HEIGHT NOTES:	
* ARCHITECTURAL FOOTING AND FOUNDATION ELEVATION ARE RELATIVE TO ARCHITECTURAL MAIN FLOOR OF + 0'-0" ELEVATION.	
* ARCHITECTURAL + 0'-0" ELEVATION = SURVEY / CIVIL ENGINEERING SITE PLAN "FF" FLOOR ELEVATION. COORDINATE WITH CIVIL DRAWINGS.	

THE BLACK DAHLIA
(NEW CONSTRUCTION CUSTOM HOME)
2387 SOUTH VILLAGE Dr. (LOT 2) SANTA CLARA, UT 84765
PREPARED FOR MR. & MRS. LETHIN (CLIENTS OF MARKAY JOHNSON CONST.)

PROJECT NUMBER: 25-01
DATE
21-Aug-2025

#	REVISION	DATE
0.	ORIGINAL ISSUE	8.19.25
1.		
2.		
3.		

SHEET TITLE

EXTERIOR
ELEVATIONS


SHEET NUMBER

A.202

(24 x 36 : ARCH D)

PLANS PRINTED ON 11 x 17 PAPER ARE 1/2 THE SCALE NOTED

THESE PLANS ARE INSTRUMENTS OF PROFESSIONAL SERVICE AND ARE THE INTELLECTUAL PROPERTY OF ROUGE DESIGNS LLC. AND ARE PROTECTED BY COMMON LAW, STATUTE, AND OTHER RESERVED RIGHTS INCLUDING, BUT NOT LIMITED TO, COPYRIGHT. THESE PLANS SHALL NOT BE REPRODUCED OR USED FOR ANY OTHER PROJECT AND OR USED FOR ANY PURPOSE WITHOUT THE WRITTEN CONSENT OF ROUGE DESIGNS LLC. THE PREPARE OF THESE PLANS ASSUMES NO FINANCIAL LIABILITY RESULTING FROM ERRORS OR OMISSIONS IN THESE PLANS.

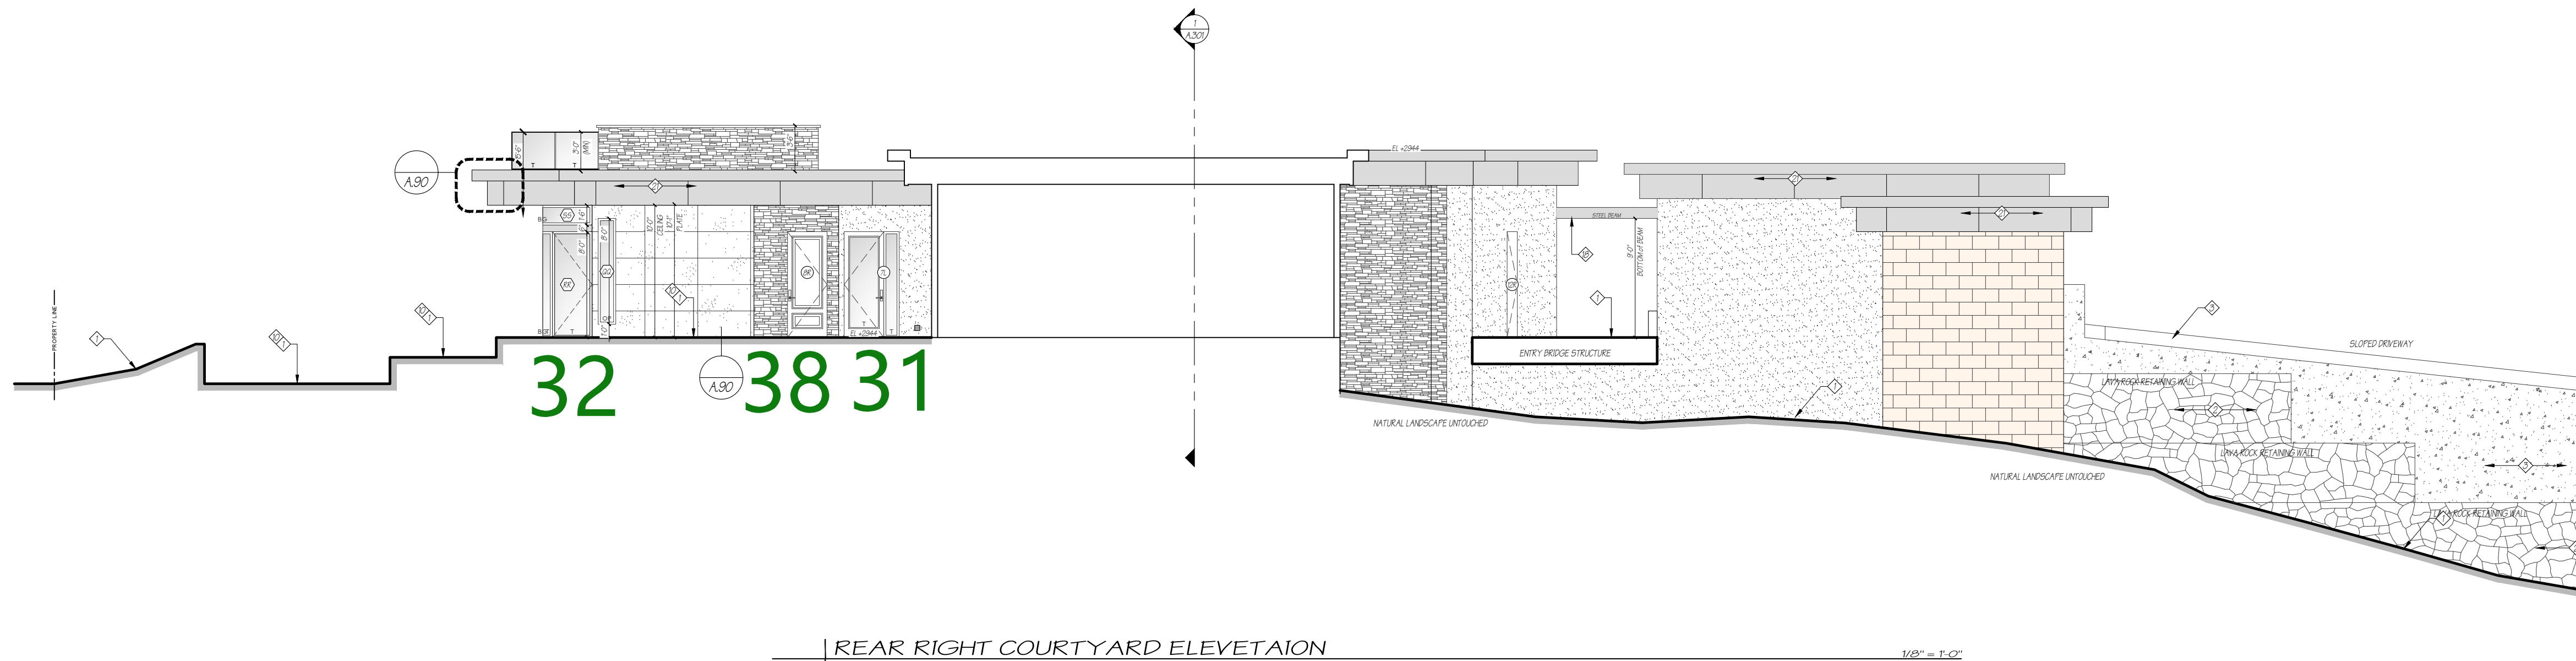

(ELEVATION MATERIAL LEGEND :

	CLUSTERED / NATURAL STONE VENEER (TOTAL SQFT : ~ 000) COLOR : (REFER TO EXTERIOR SELECTION SHEET)
	NATURAL STONE TILE (TOTAL SQFT : ~ 000) COLOR : (REFER TO EXTERIOR SELECTION SHEET)
	LIGHT WEIGHT CONCRETE TILE VENEER (TOTAL SQFT : ~ 000) COLOR : (REFER TO EXTERIOR SELECTION SHEET)
	STUCCO HARD COAT (ULTRA SMOOTH / SHINY TEXTURE) (TOTAL SQFT : ~ 000) COLOR : (REFER TO EXTERIOR SELECTION SHEET)
	STEPPED METAL FASCIA / DRIP EDGE (SOLID) METAL FASCIA (TOTAL SQFT : ~ 000) COLOR : (REFER TO EXTERIOR SELECTION SHEET)
	WOODEN EXTERIOR CLADDING (TOTAL SQFT : ~ 000) COLOR : (REFER TO EXTERIOR SELECTION SHEET)
	LAVA ROCK VENEER OR BOLLIER LAVA ROCK (TOTAL SQFT : ~ 000) COLOR : (REFER TO EXTERIOR SELECTION SHEET)

GARAGE DOORS COLOR : _____ MANUF. STANDARD BRONZE
EXTERIOR WINDOW FRAME COLOR : _____ MANUF. STANDARD DARK BRONZE
EXTERIOR DOORS COLOR : _____ MANUF. STANDARD DARK BRONZE
SLOTTED : _____ REFER TO EXTERIOR SELECTION SHEET
PARAPET CAP : _____ REFER TO EXTERIOR SELECTION SHEET



** INSTALL MATERIAL TYPES PER MANUFACTURE RECOMMENDATIONS, ATTACH VENEER PER GENERAL STRUCTURAL NOTES, WHERE APPLIES PROVIDE AND INSTALL REQUIRED CONTROL JOINTS PER MANUF. **

EXTERIOR ELEVATION GENERAL NOTES :

- CONTRACTOR IS RESPONSIBLE FOR PREPARATION, WATERPROOFING, AND INSTALLATION OF CLADDING / RAIN SCREEN / STUCCO SCRATCH COAT / EIFS ASSEMBLY PER MANUF. RECOMMENDATIONS. FILL ALL JOINTS WITH MATCHING CAULK.
- NO MECHANICAL EQUIPMENT, VENT STACKS, FASTENERS, SNOW EXETER, FLUENCE FLUE, METAL WORK AND OTHER VISUAL ELEMENTS SHALL BE LOCATED ON THE FRONT OF THE HOME.
- INSTALL ALL EXTERIOR MATERIAL / CLADDING PER MANUF. RECOMMENDATIONS.
- ALL SEALANT / FRAMING SYSTEMS AND GASKETS AND WATERPROOFING MEMBRANE SHALL BE ASSEMBLED IN SUCH A MANNER TO PROVIDE A HIGH QUALITY WEATHERPROOFING BUILDING ENCLOSURE.
- ALL SEALANT / CAULKING COLOR SHALL MATCH THE ADJACENT MATERIAL OR OTHERWISE NOTED.
- ALL FASTENERS ARE TO BE CONCEALED, EFFECT AS SPECIFIED. ALL BUTT JOINTS ARE TO HAVE CONCEALED / PACKED UP TO 80% WITH CAPTIVE SEALANT.
- TOP OF THE FOUNDATION IS TO EXTEND ABOVE FINISH GRADE 6IN (MIN).
- ALL FLASHING, VENTING AND PIPES ARE TO BE PAINTED TO MATCH ADJACENT MATERIALS.
- NO REFLECTIVE EXTERIOR MATERIAL ARE ALLOWED.
- PROVIDE OPAQUE GLAZING AT BATHROOM / WATERCLOSET LOCATION(S). VERIFY W/ INTERIOR DESIGN TEAM.
- EXTERIOR LIGHTING SHALL SHADOW AND POSITIONED SO AS TO REFLECT LIGHT AWAY FROM ADJACENT RESIDENCE AND ROADWAYS.

ELEVATION HEIGHT NOTES :

- ARCHITECTURAL FOOTING AND FOUNDATION ELEVATION ARE RELATIVE TO ARCHITECTURAL MAIN FLOOR OF + 0'-0" ELEVATION.
- ARCHITECTURAL + 0'-0" ELEVATION = SURVEY / CIVIL ENGINEERING SITE PLAN "FF" FLOOR ELEVATION. COORDINATE WITH CIVIL DRAWINGS.

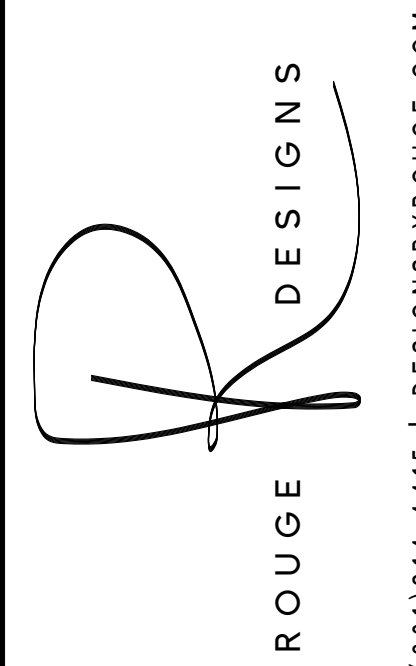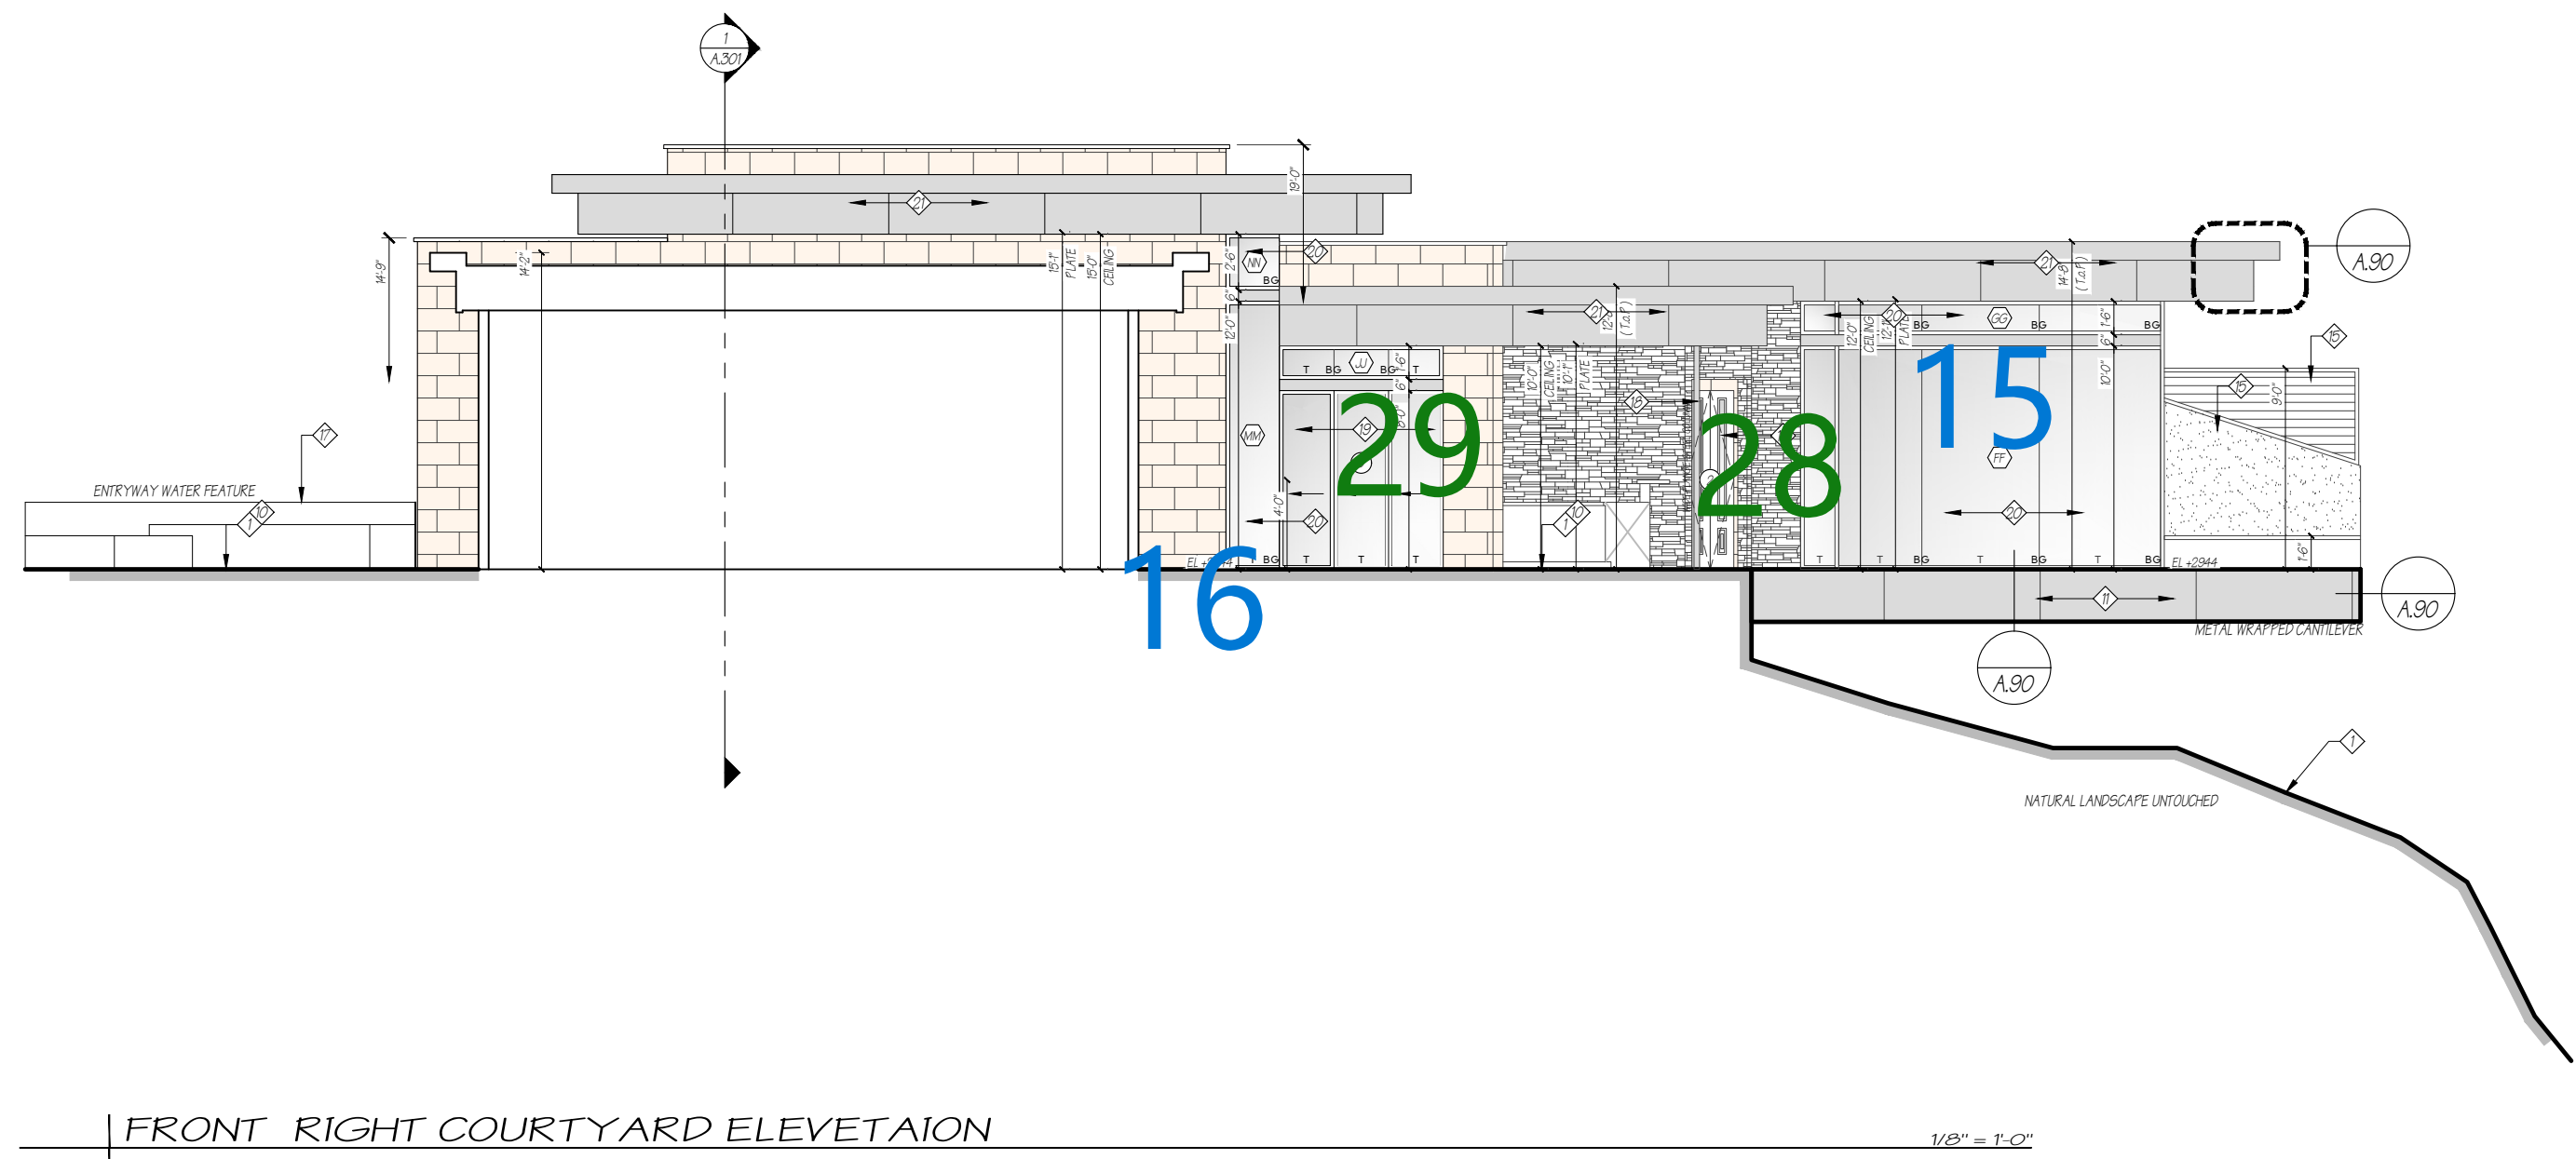

THESE PLANS MAY ONLY BE USED FOR THIS SPECIFIC ADDRESS AND PROJECT ONLY. THESE PLANS AND DOCUMENTS ARE THE INTELLECTUAL PROPERTY OF ROUGE DESIGNS LLC. AND ANY REUSE OR FURTHER DISTRIBUTION THEREOF IN PART OR IN WHOLE WITHOUT THE WRITTEN PERMISSION OF ROUGE DESIGNS LLC IS STRICTLY PROHIBITED. THE DESIGN REPRESENTED BY THESE DRAWINGS IS SOLD TO THE CLIENT FOR A ONE TIME USE, UNLESS OTHERWISE AGREED UPON IN WRITING BY ARCHITECT OR ENGINEER.
© COPYRIGHT 2025 ROUGE DESIGNS LLC

THE BLACK DAHLIA
(NEW CONSTRUCTION CUSTOM HOME)
2387 SOUTH VILLAGE Dr. (LOT 2) SANTA CLARA, UT 84765
PREPARED FOR MR. & MRS. LETHIN (CLIENTS OF MARKAY JOHNSON CONST.)

PROJECT NUMBER : 25-01

DATE
21-Aug-2025

#	REVISION	DATE
0.	ORIGINAL ISSUE	8.19.25
1.		
2.		
3.		

SHEET TITLE

EXTERIOR
ELEVATIONS
(COURTYARD)

SHEET NUMBER

A.203

(24 x 36 : ARCH D)

PLANS PRINTED ON 11 x 17 PAPER ARE 1/2 THE SCALE NOTED